


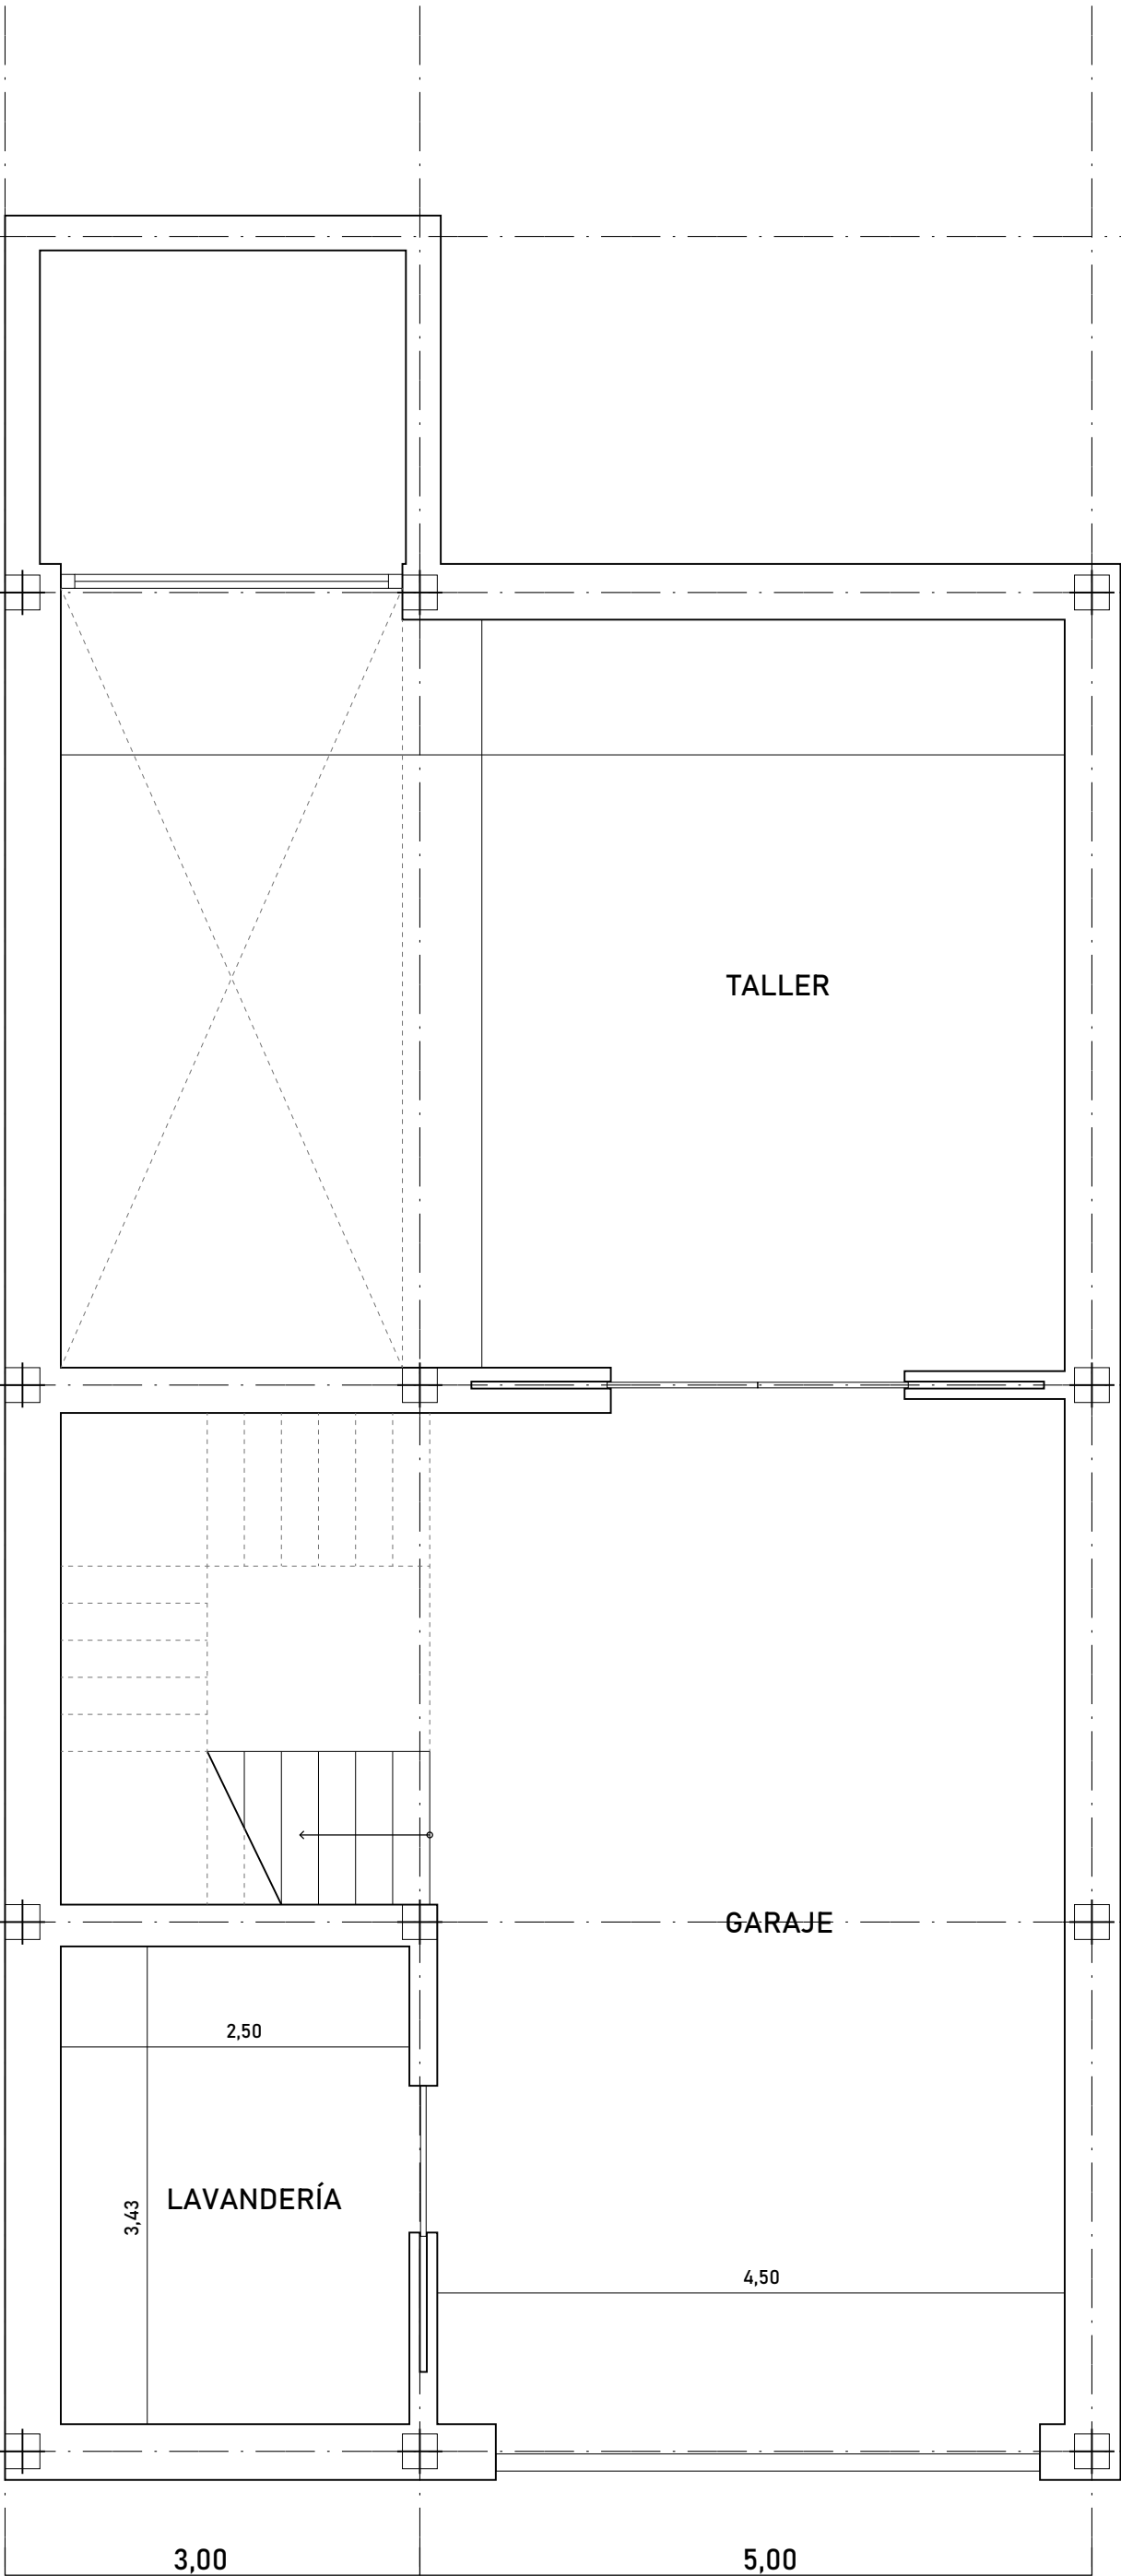


A


B

C

DENOMINACIÓN			
SEMISÓTANO			
PROMOTORES		ESTUDIANTES DE ARQUITECTURA	
ANTONIO VELA COSSIO		JAVIER PÉREZ PELLÓN ALEJANDRO MARTÍN SANCHEZ	
ESCALA	1/50	SUSTITUYE A	PLANO 1

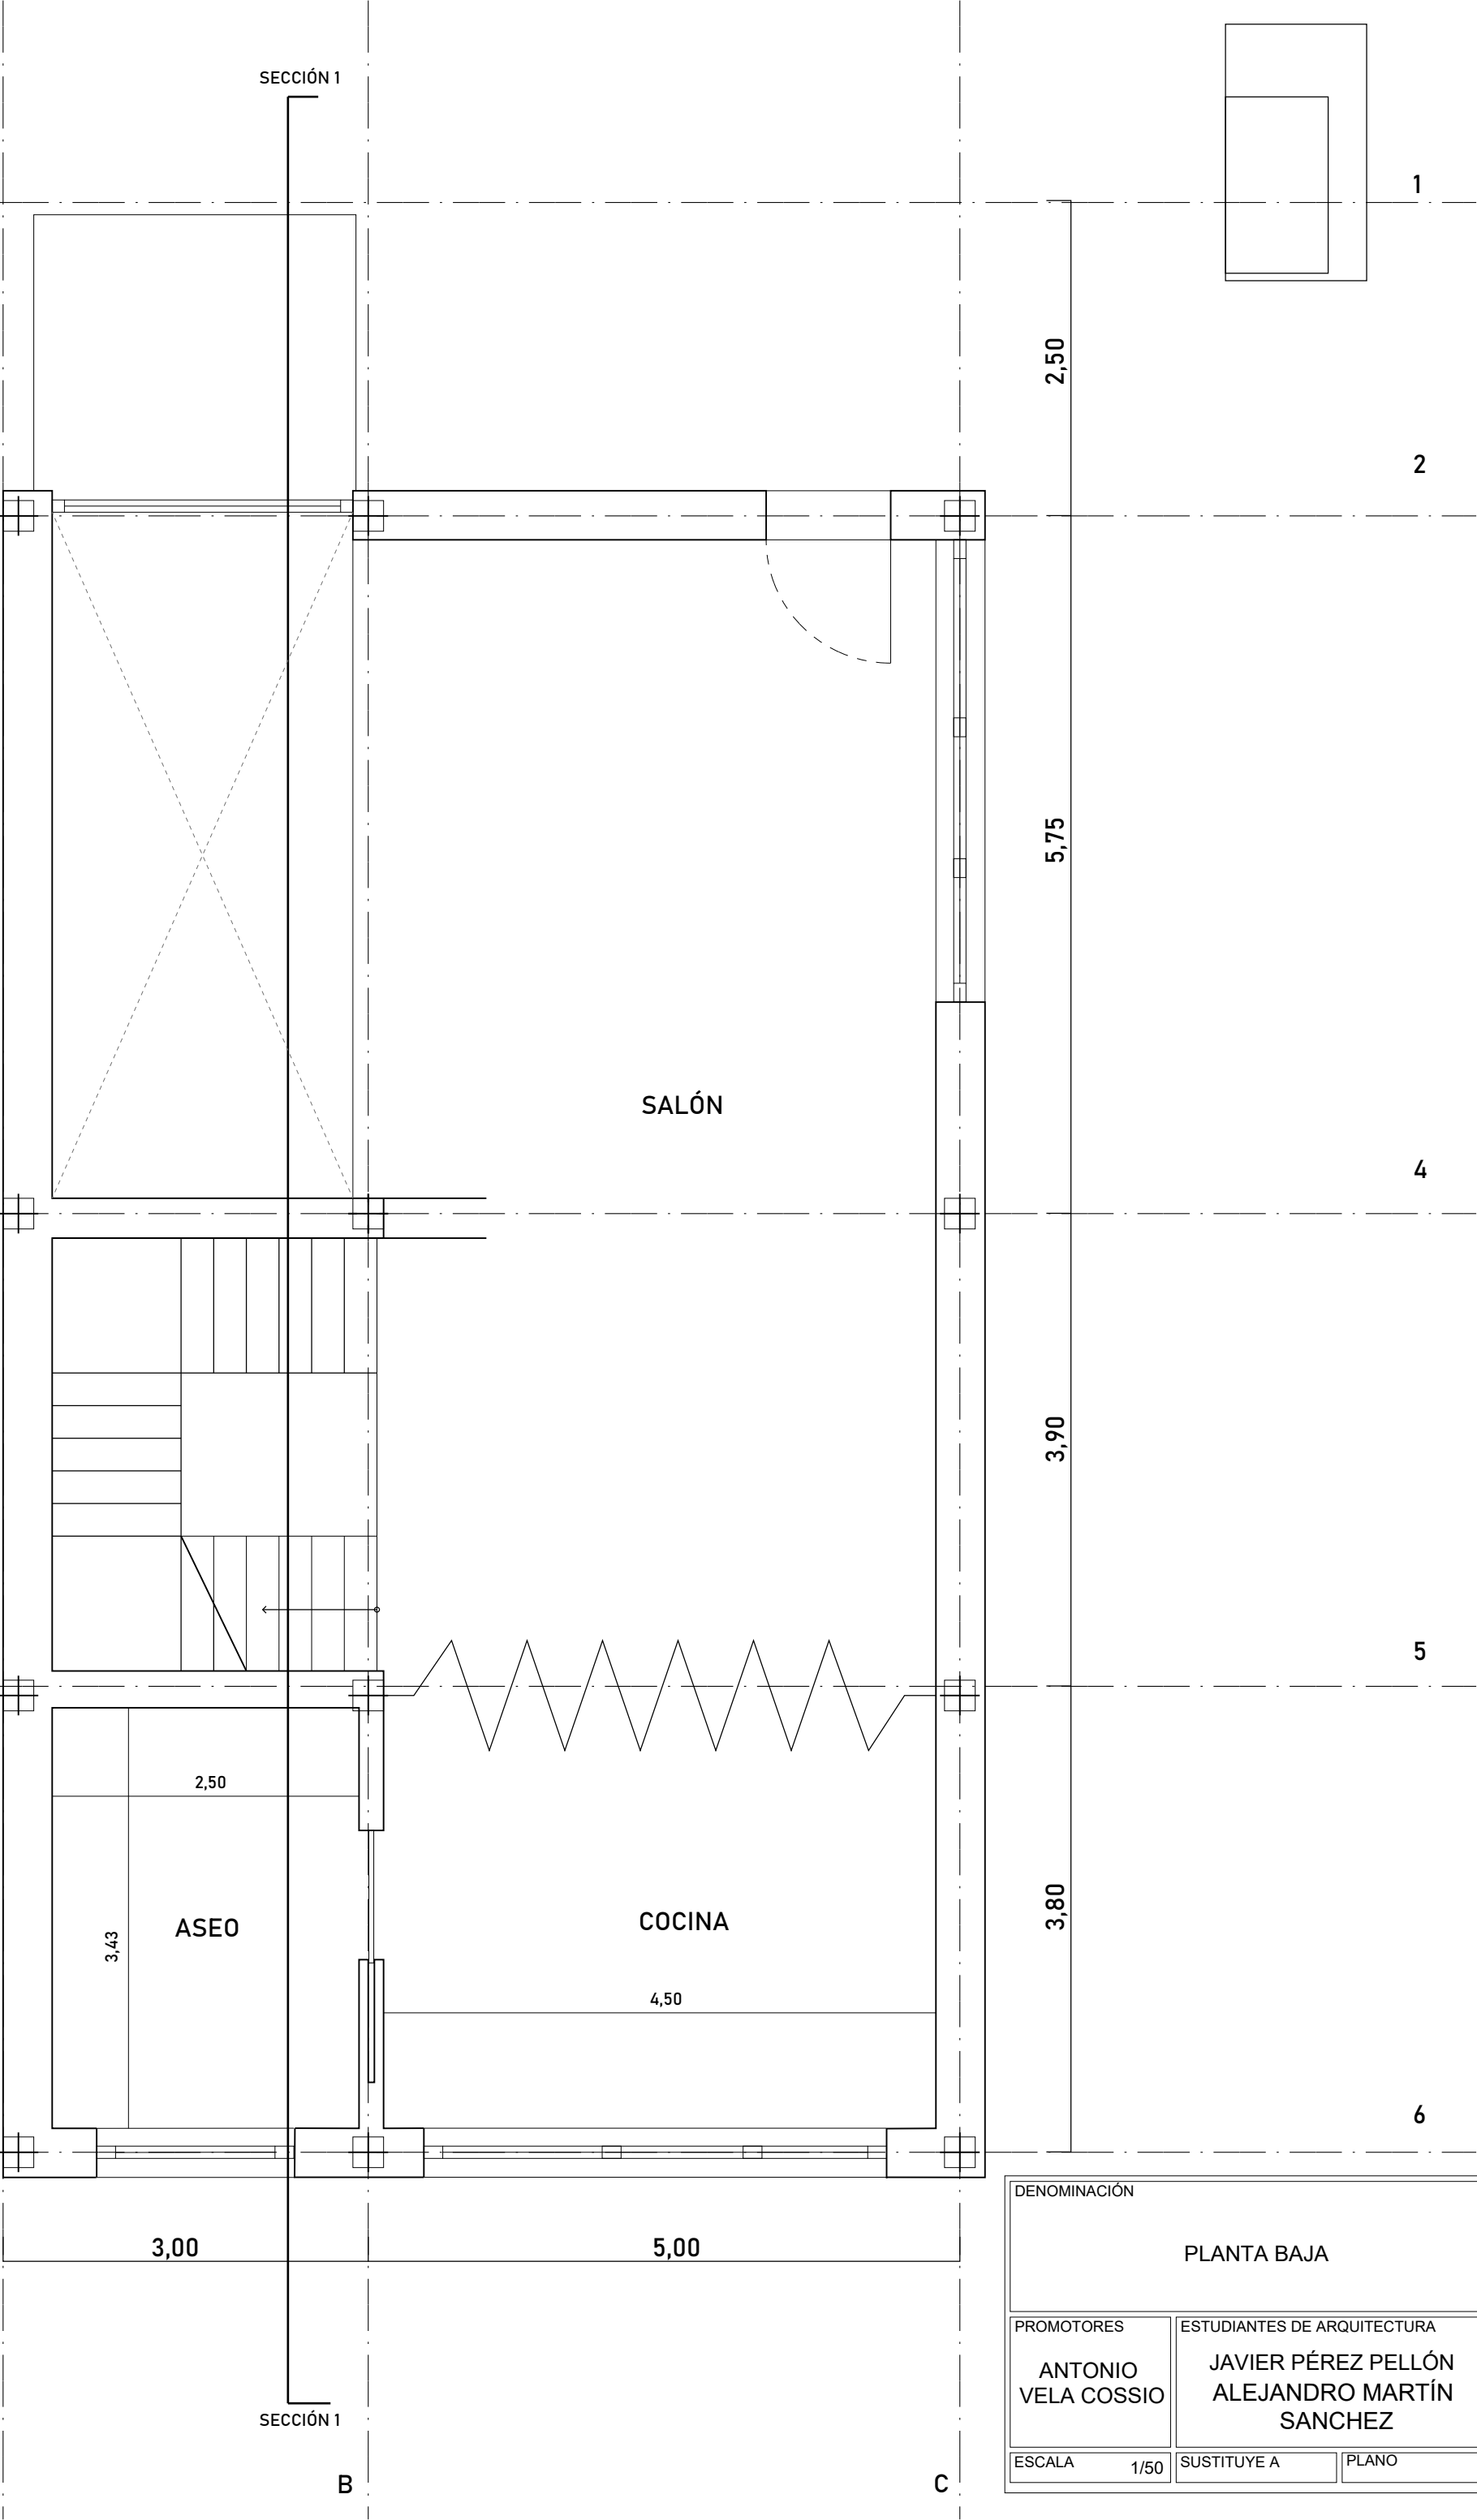

DENOMINACIÓN			
PLANTA BAJA			
PROMOTORES		ESTUDIANTES DE ARQUITECTURA	
ANTONIO VELA COSSIO		JAVIER PÉREZ PELLÓN ALEJANDRO MARTÍN SANCHEZ	
ESCALA	1/50	SUSTITUYE A	PLANO 2

 

1

2

4

5



6

A

B

C

DENOMINACIÓN			
PLANTA 1			
PROMOTORES		ESTUDIANTES DE ARQUITECTURA	
ANTONIO VELA COSSIO		JAVIER PÉREZ PELLÓN ALEJANDRO MARTÍN SANCHEZ	
ESCALA	1/50	SUSTITUYE A	PLANO 3

 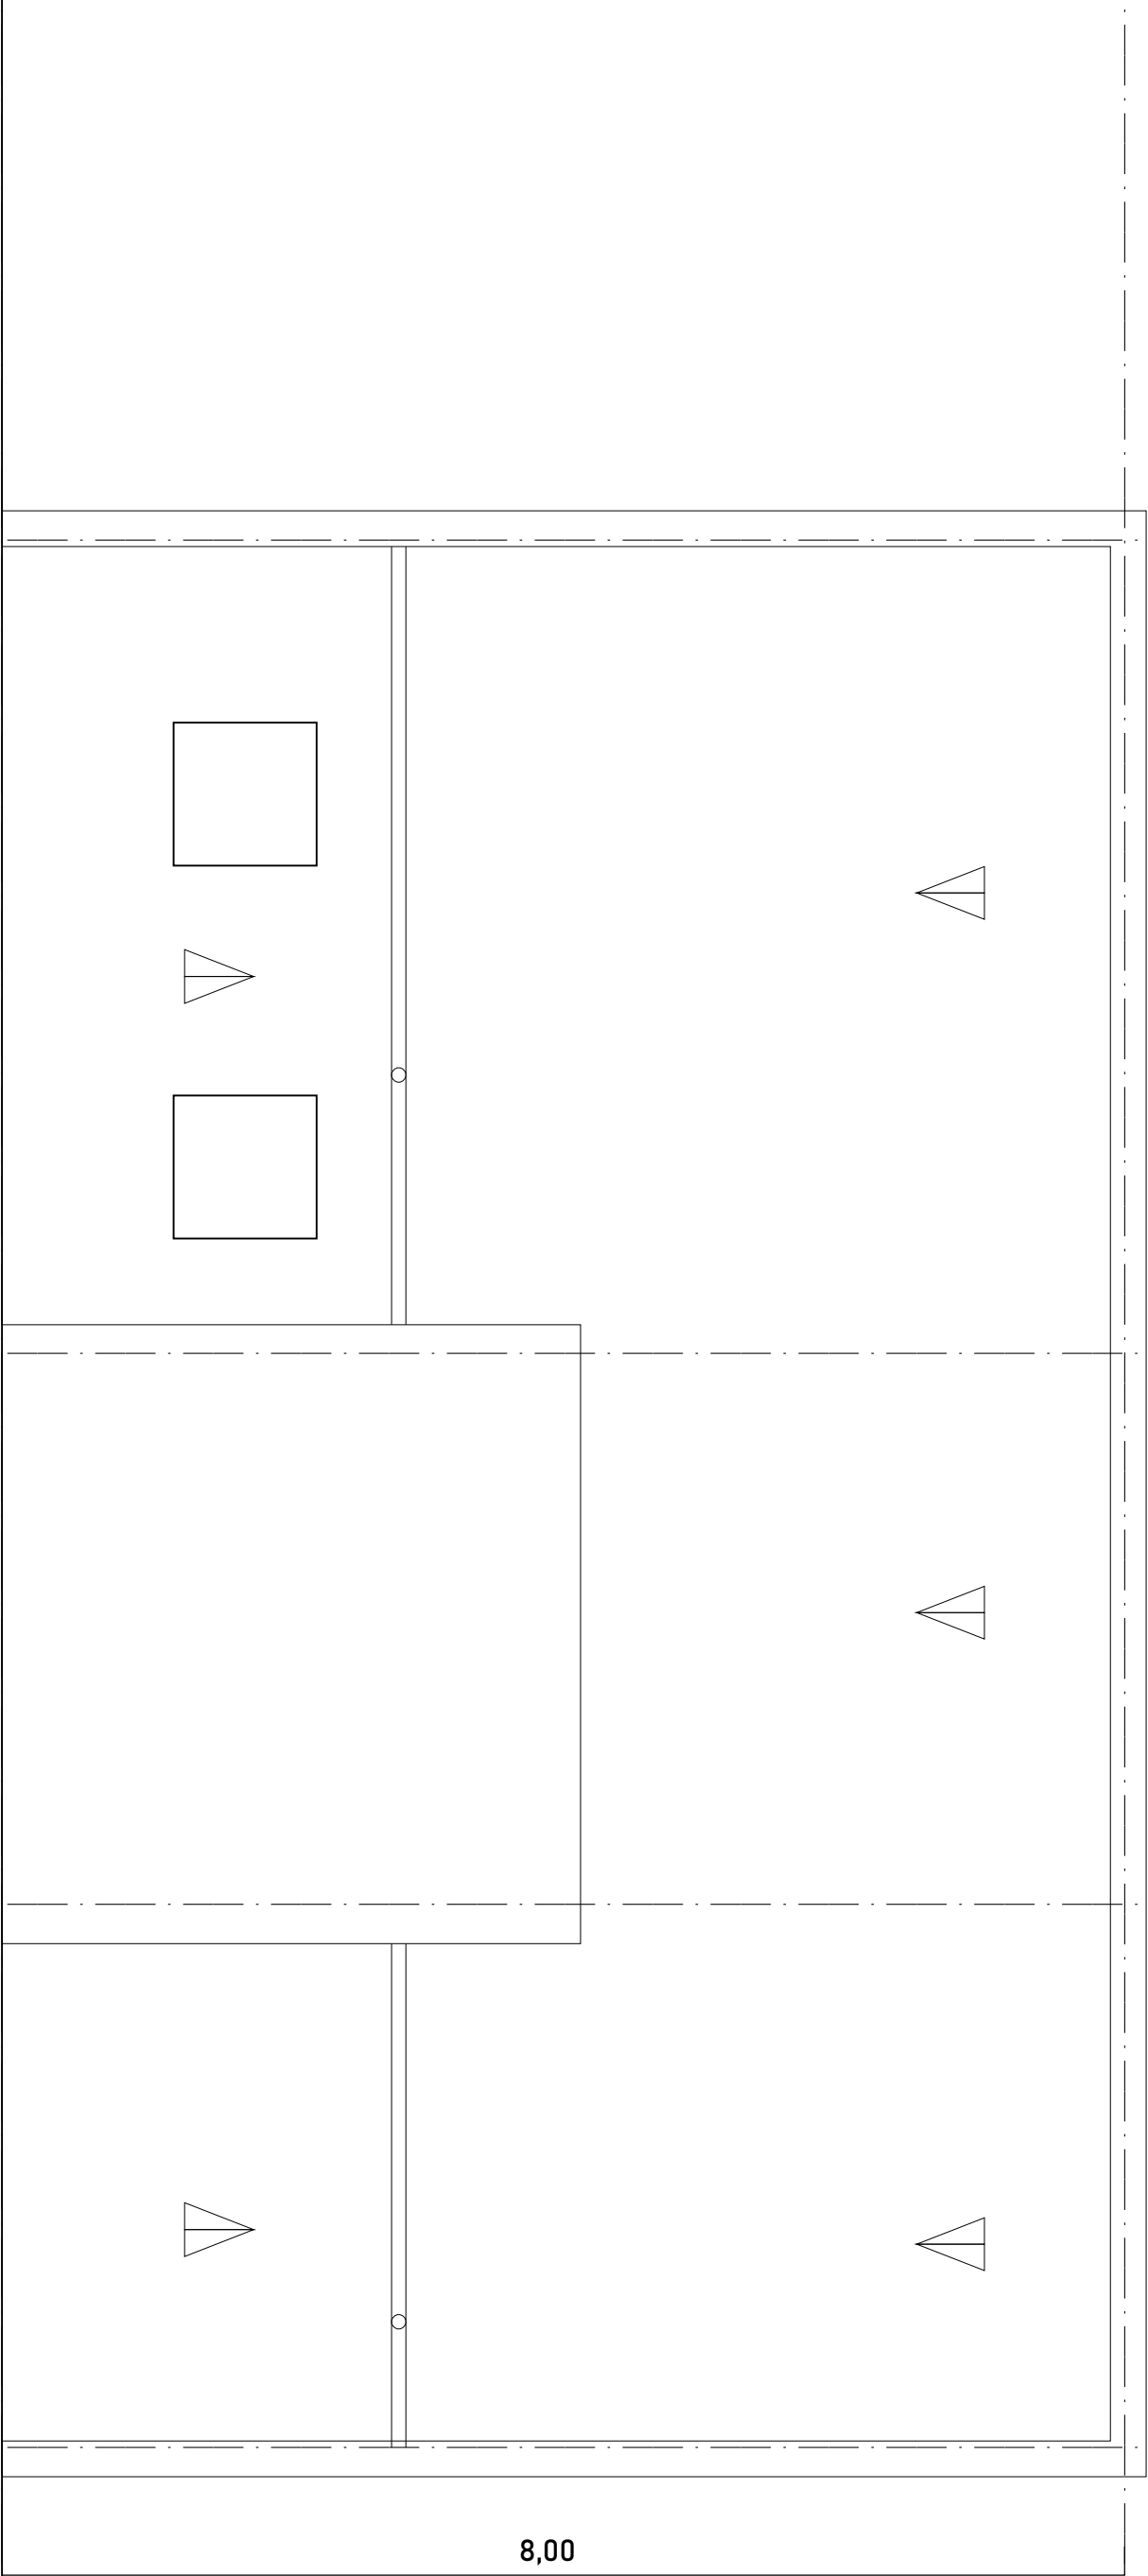

2

4


5

6


A

C


DENOMINACIÓN			
PLANO DE CUBIERTAS			
PROMOTORES		ESTUDIANTES DE ARQUITECTURA	
ANTONIO VELA COSSIO		JAVIER PÉREZ PELLÓN ALEJANDRO MARTÍN SANCHEZ	
ESCALA	1/50	SUSTITUYE A	PLANO 4

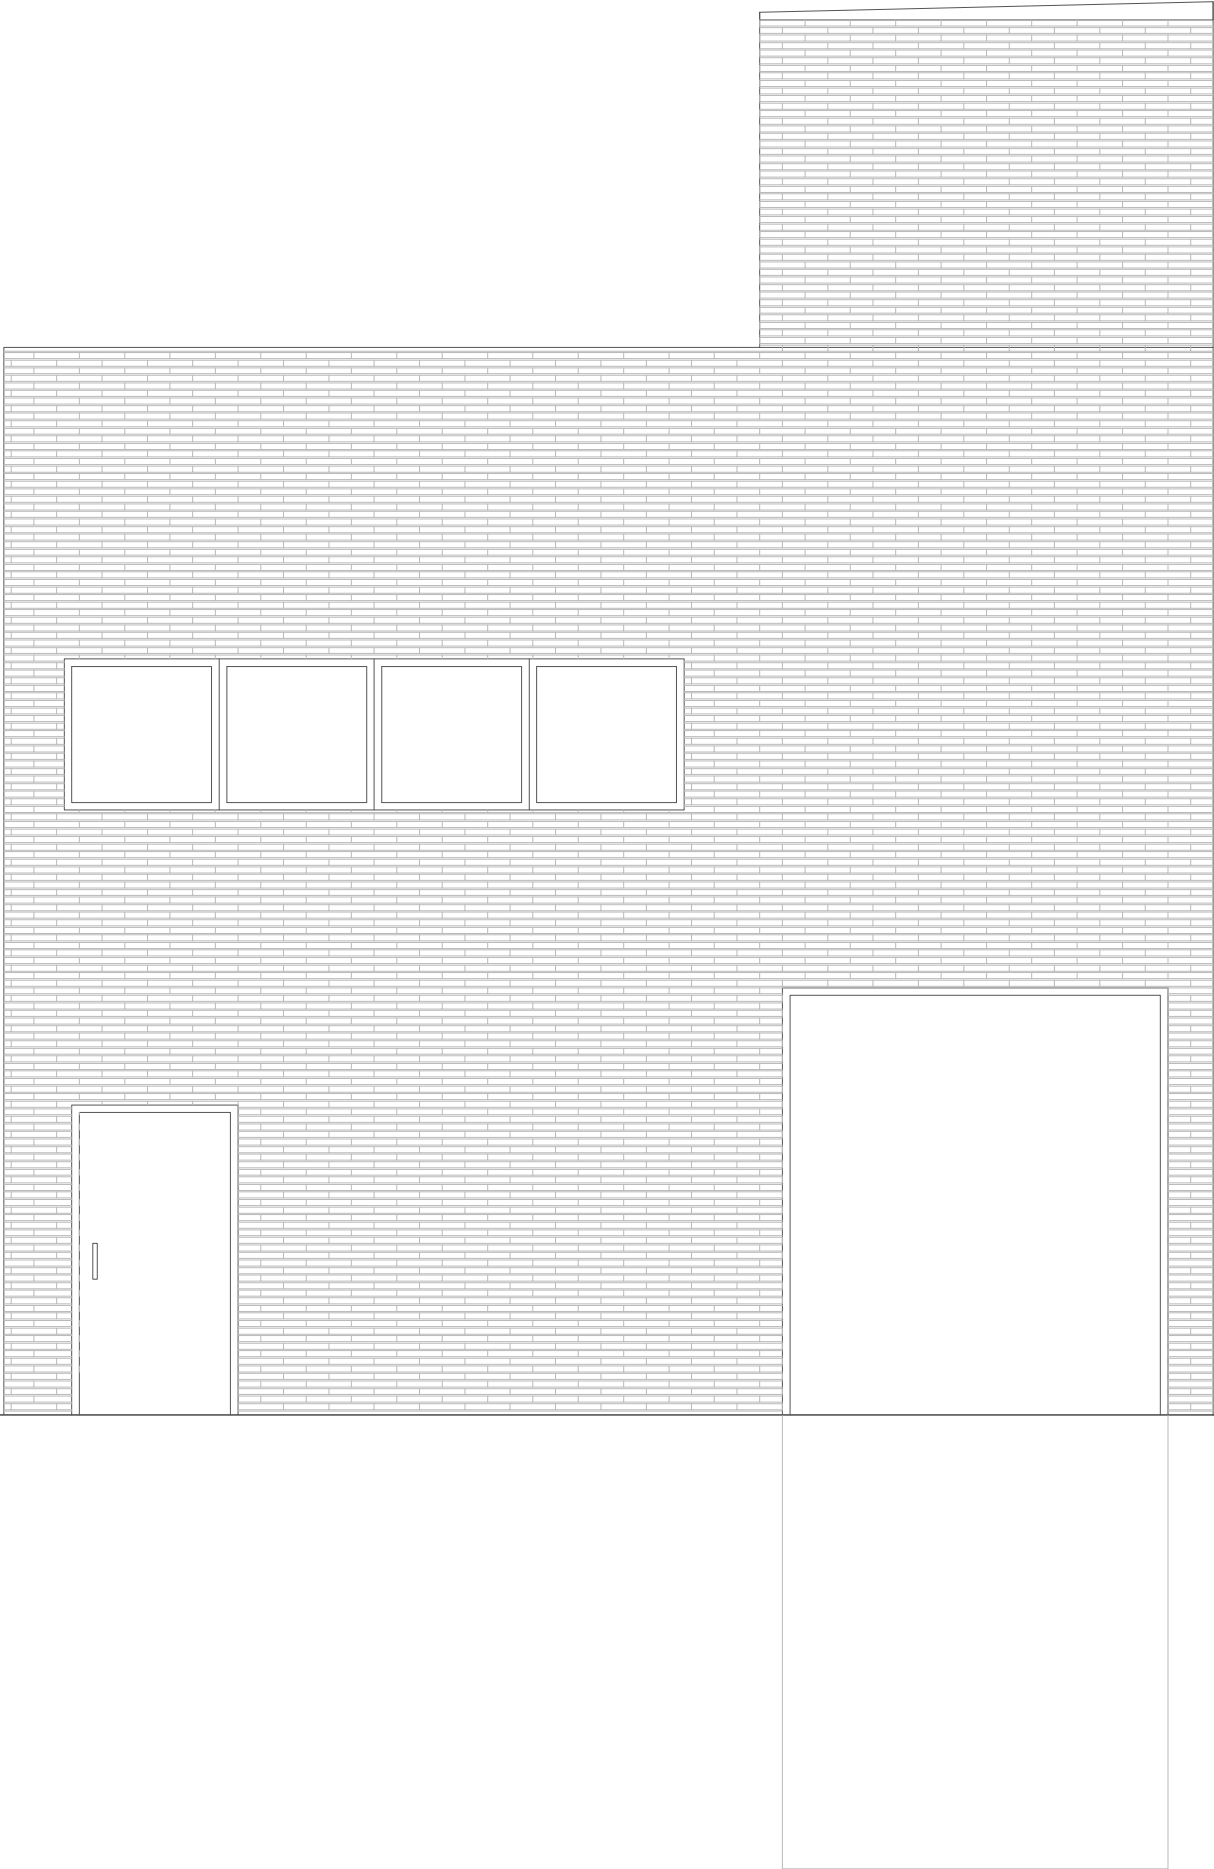


DENOMINACIÓN			
ALZADO NORESTE			
PROMOTORES		ESTUDIANTES DE ARQUITECTURA	
ANTONIO VELA COSSIO		JAVIER PÉREZ PELLÓN ALEJANDRO MARTÍN SANCHEZ	
ESCALA	1/50	SUSTITUYE A	PLANO 5

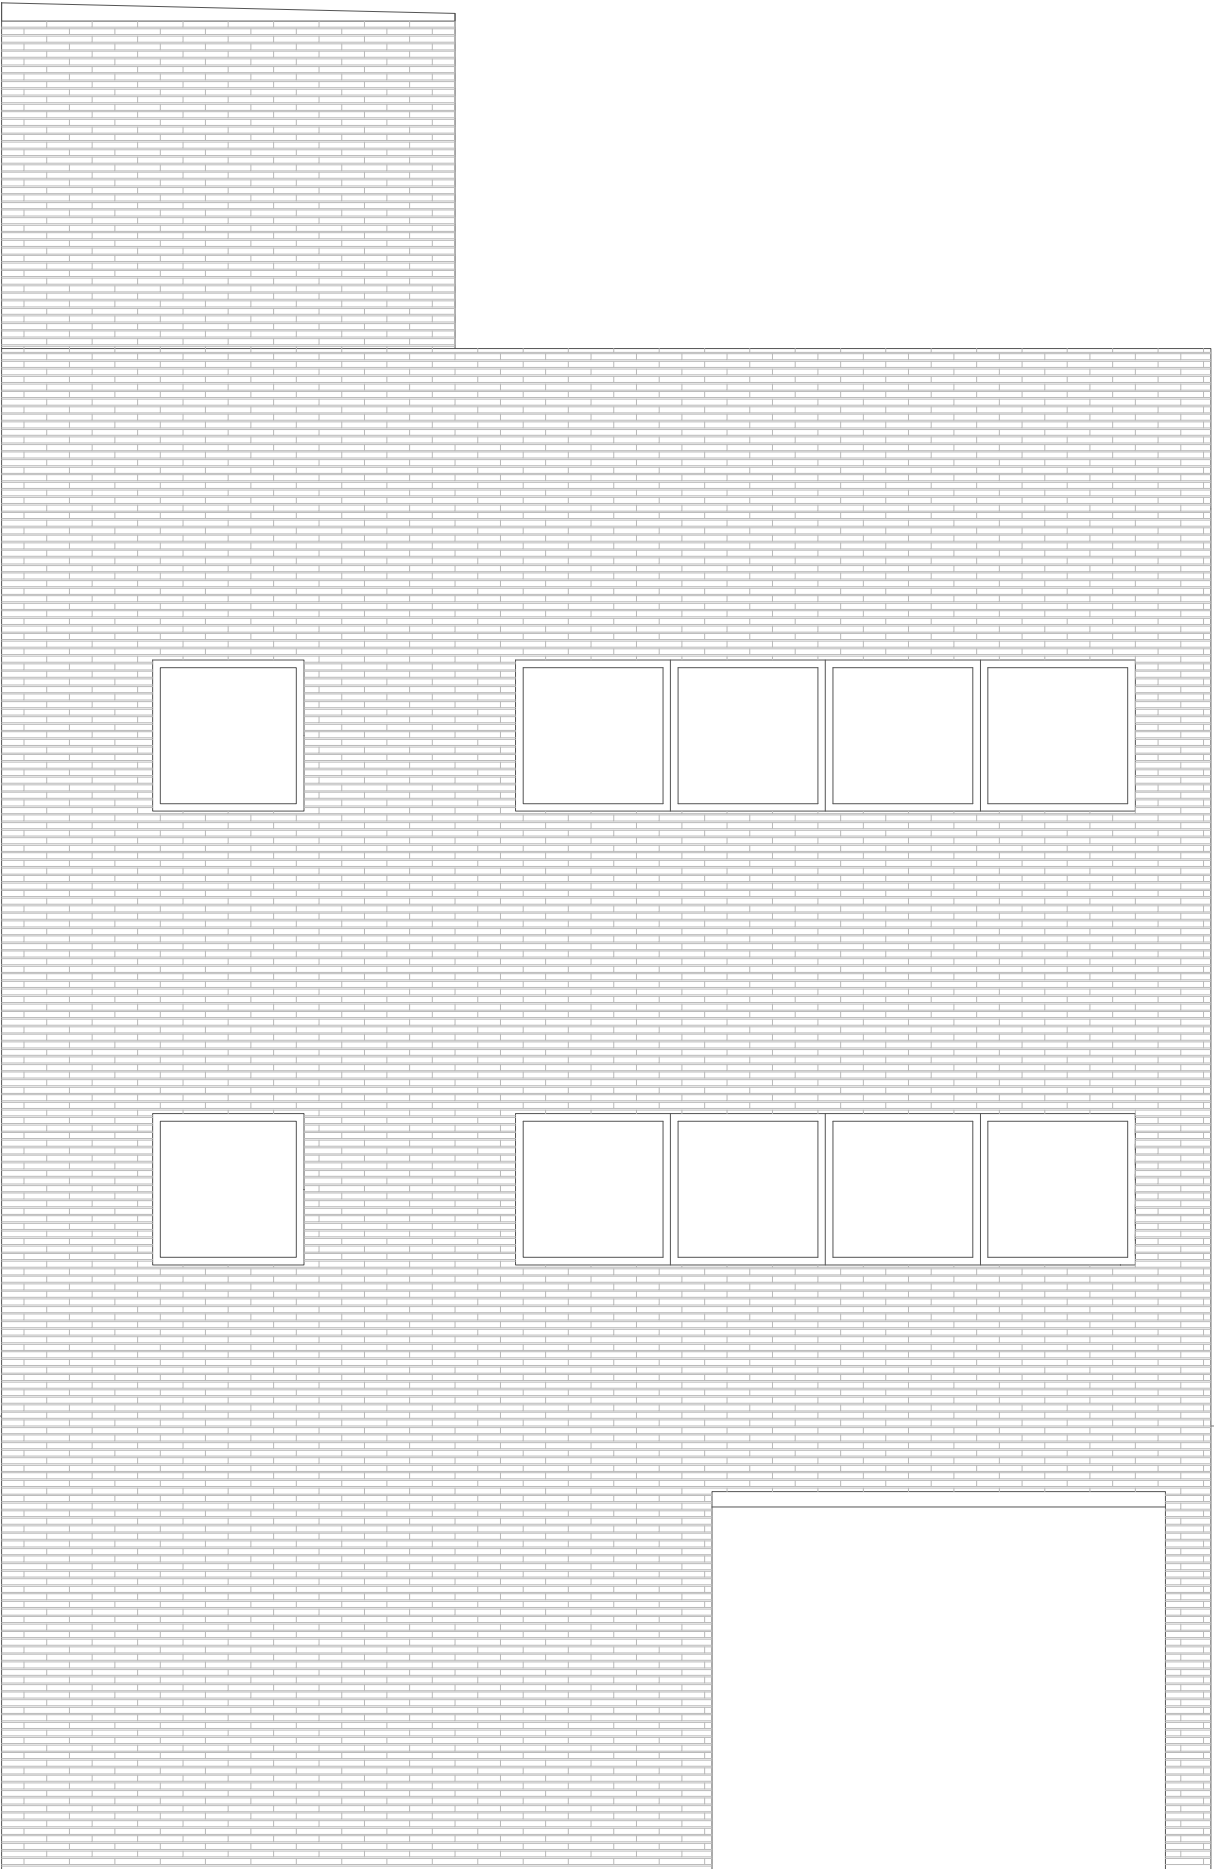


DENOMINACIÓN			
ALZADO SUROESTE			
PROMOTORES		ESTUDIANTES DE ARQUITECTURA	
ANTONIO VELA COSSIO		JAVIER PÉREZ PELLÓN ALEJANDRO MARTÍN SANCHEZ	
ESCALA	1/50	SUSTITUYE A	PLANO 6

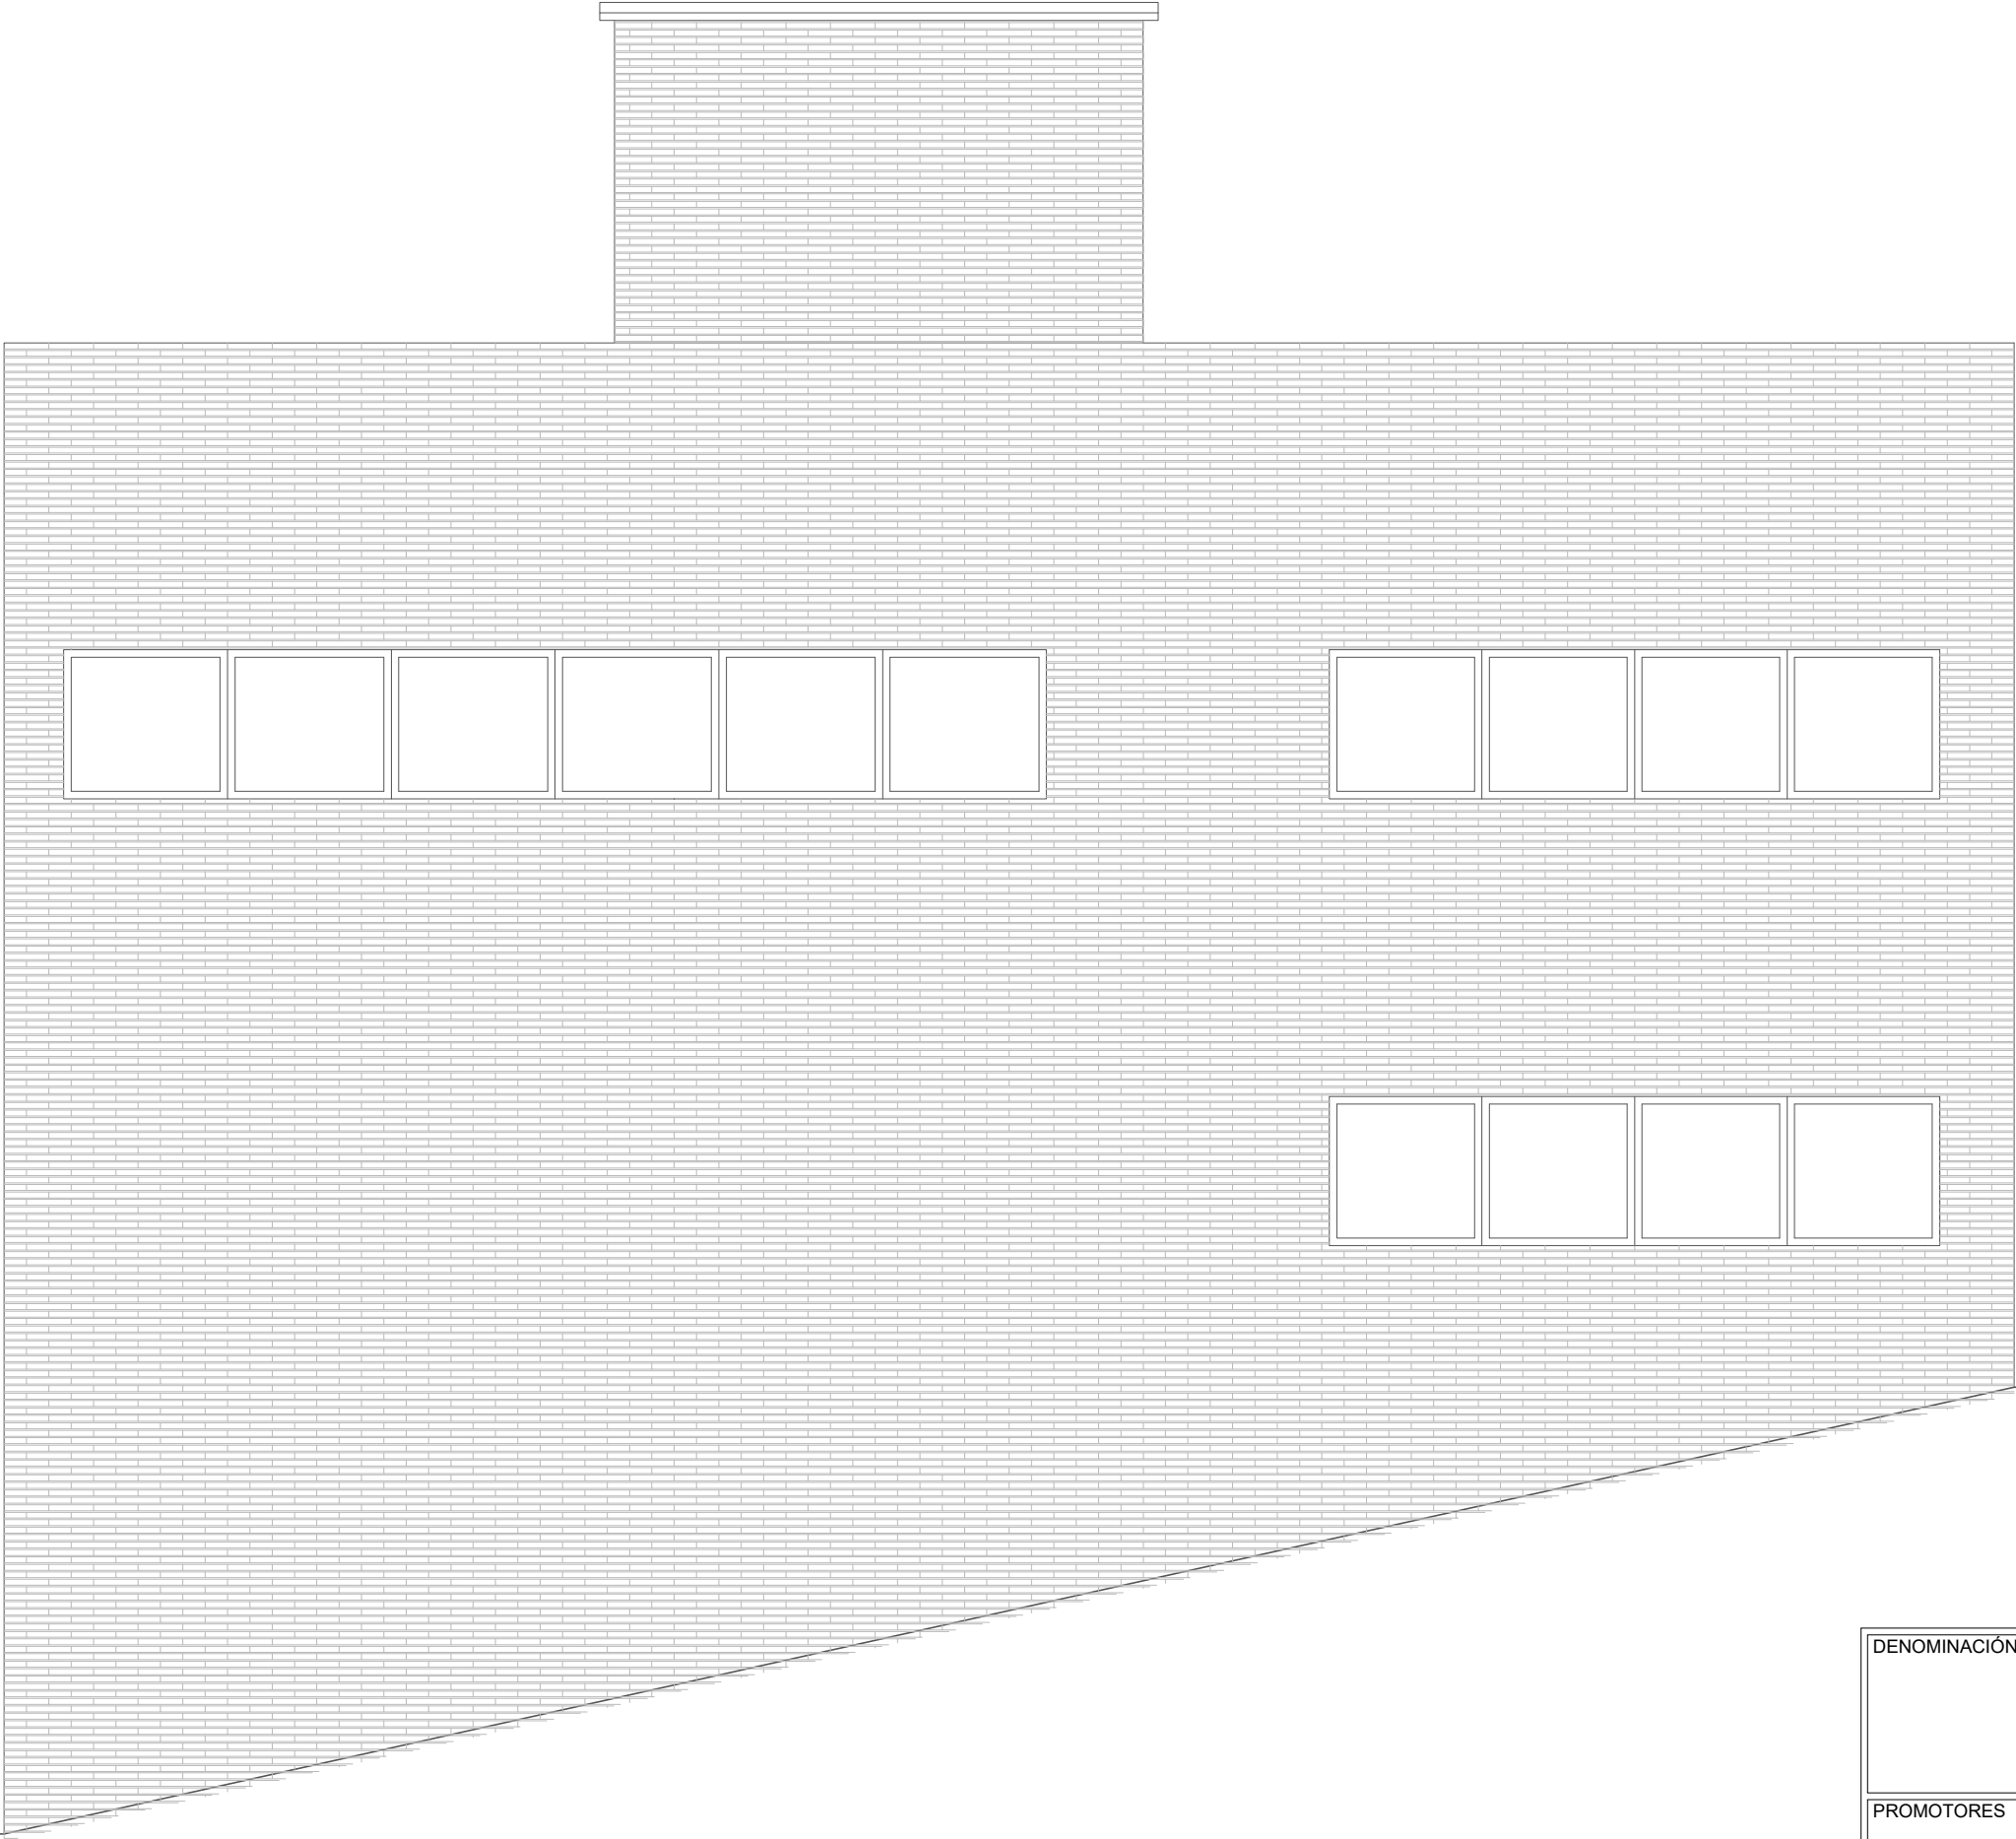


DENOMINACIÓN			
ALZADO SURESTE			
PROMOTORES		ESTUDIANTES DE ARQUITECTURA	
ANTONIO VELA COSSIO		JAVIER PÉREZ PELLÓN ALEJANDRO MARTÍN SANCHEZ	
ESCALA	1/50	SUSTITUYE A	PLANO 7

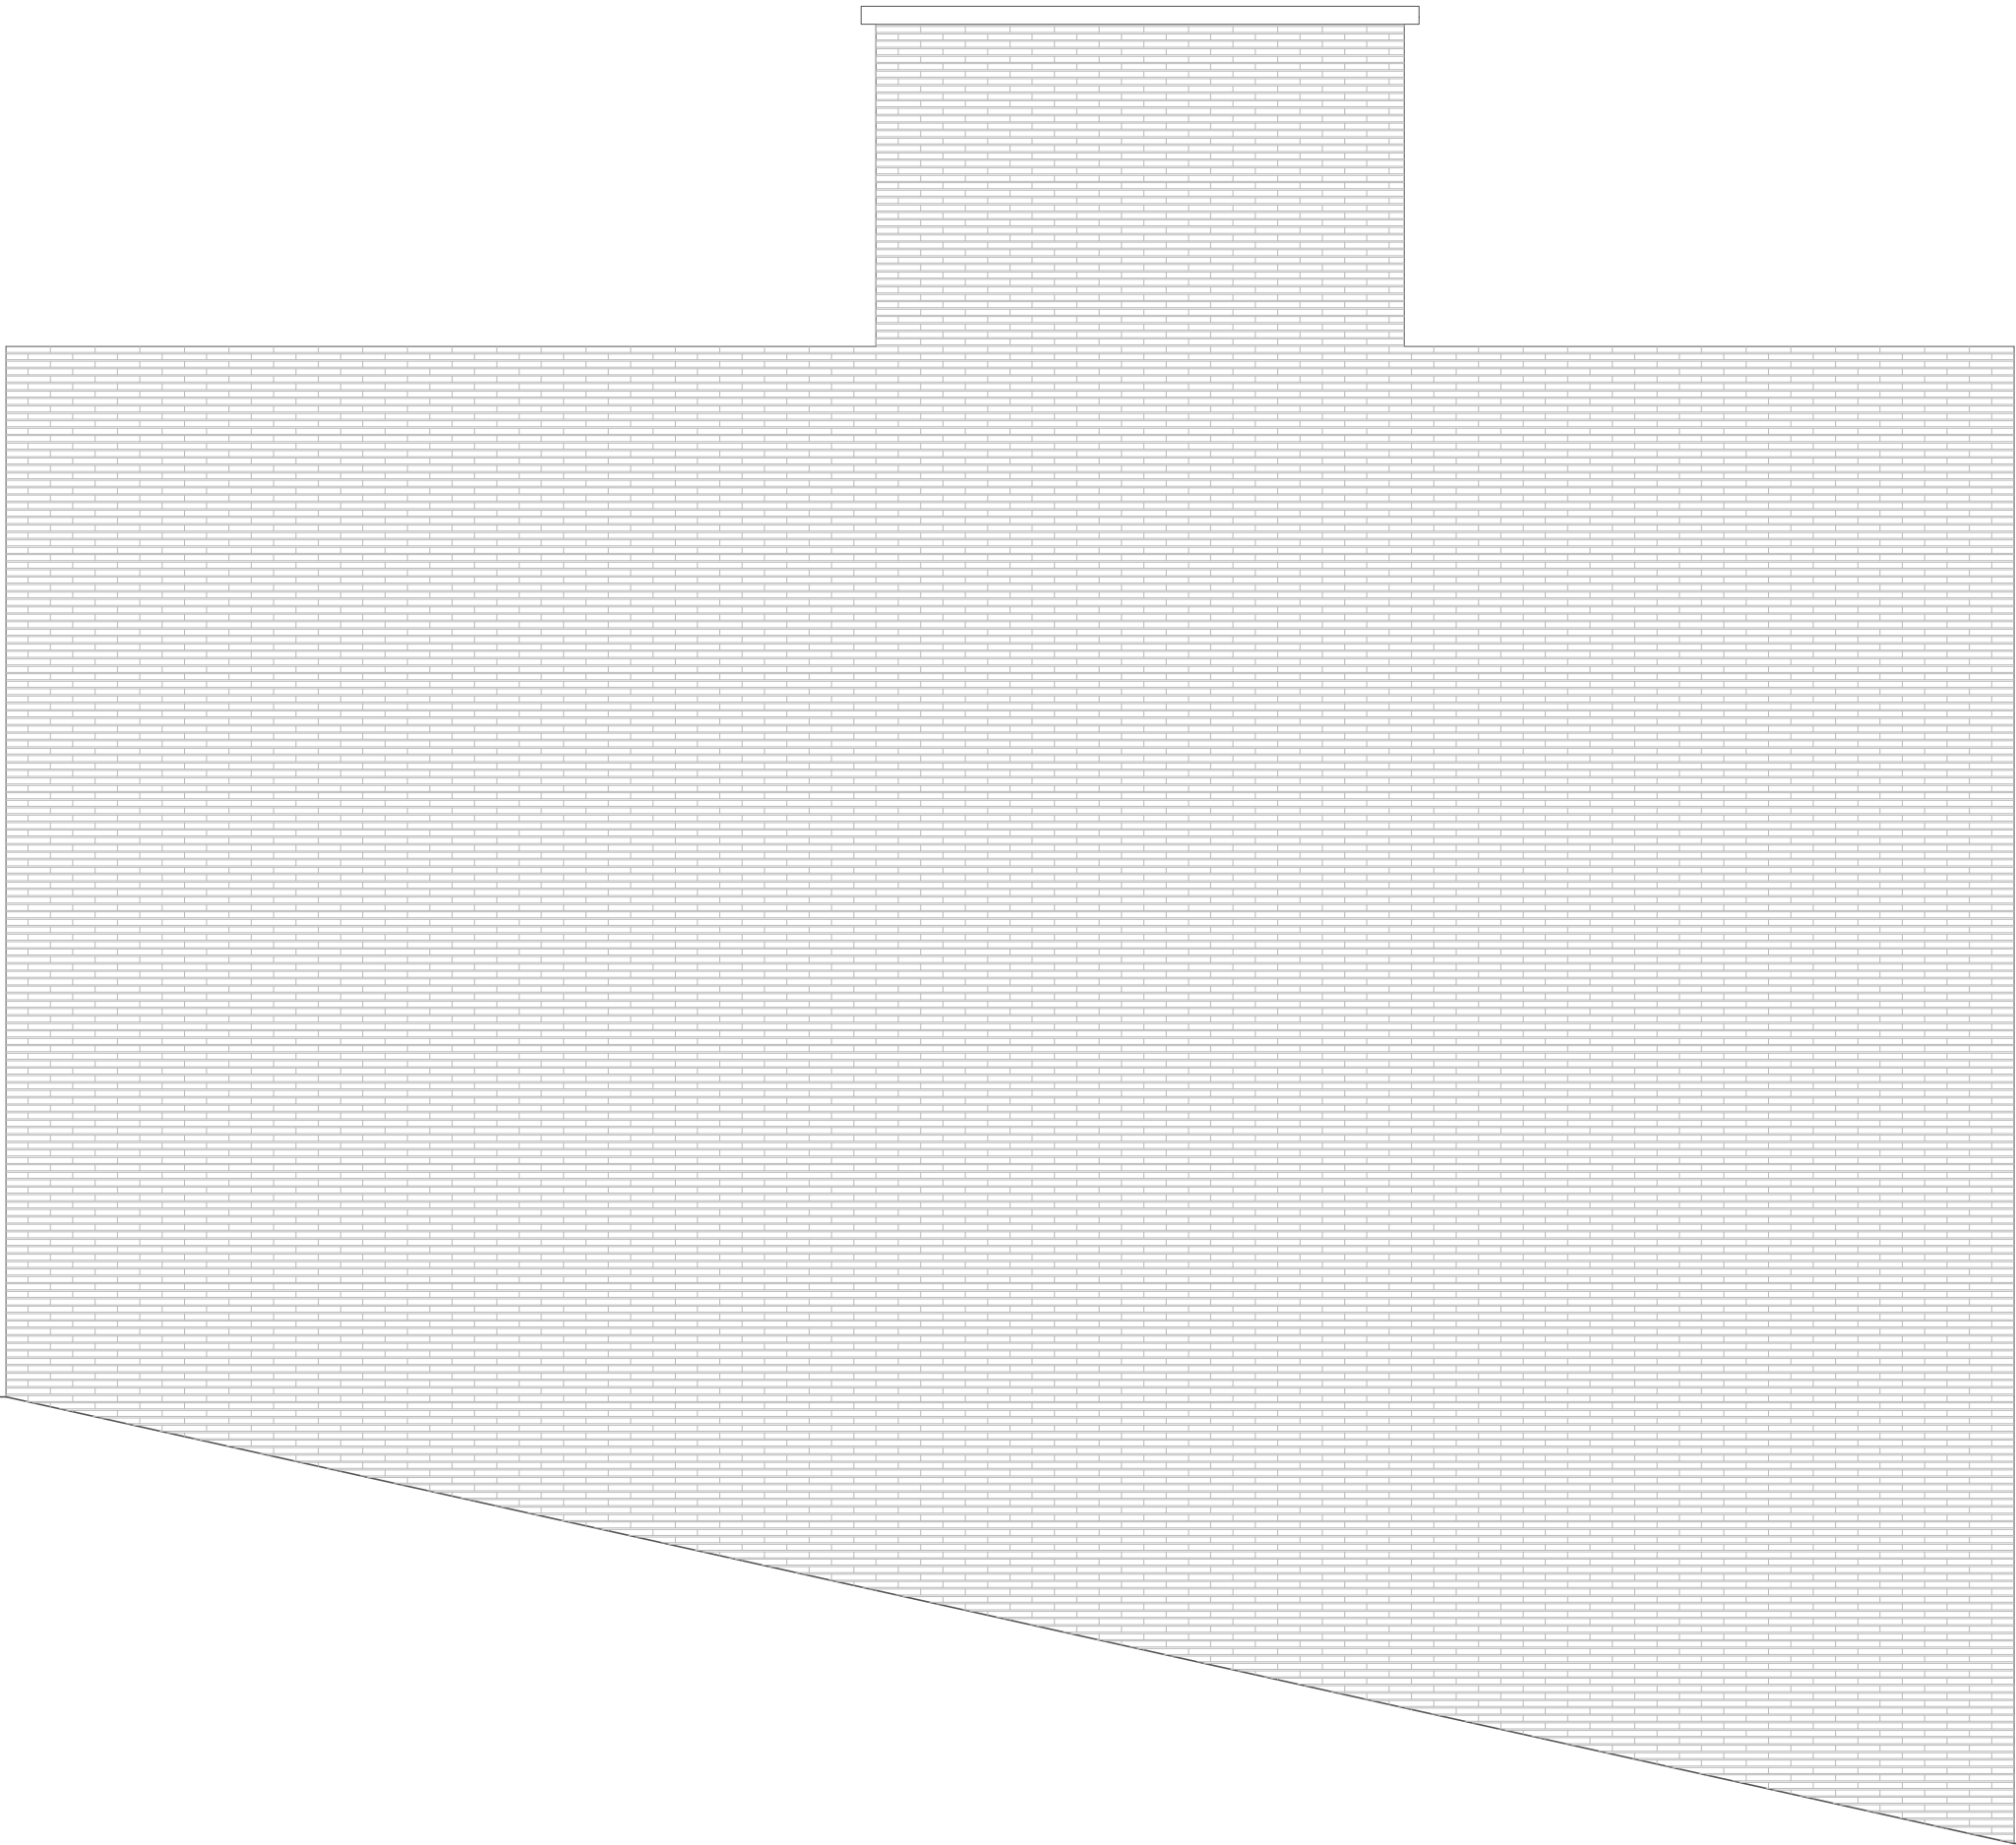


DENOMINACIÓN			
ALZADO NOROESTE			
PROMOTORES		ESTUDIANTES DE ARQUITECTURA	
ANTONIO VELA COSSIO		JAVIER PÉREZ PELLÓN ALEJANDRO MARTÍN SANCHEZ	
ESCALA	1/50	SUSTITUYE A	PLANO 8

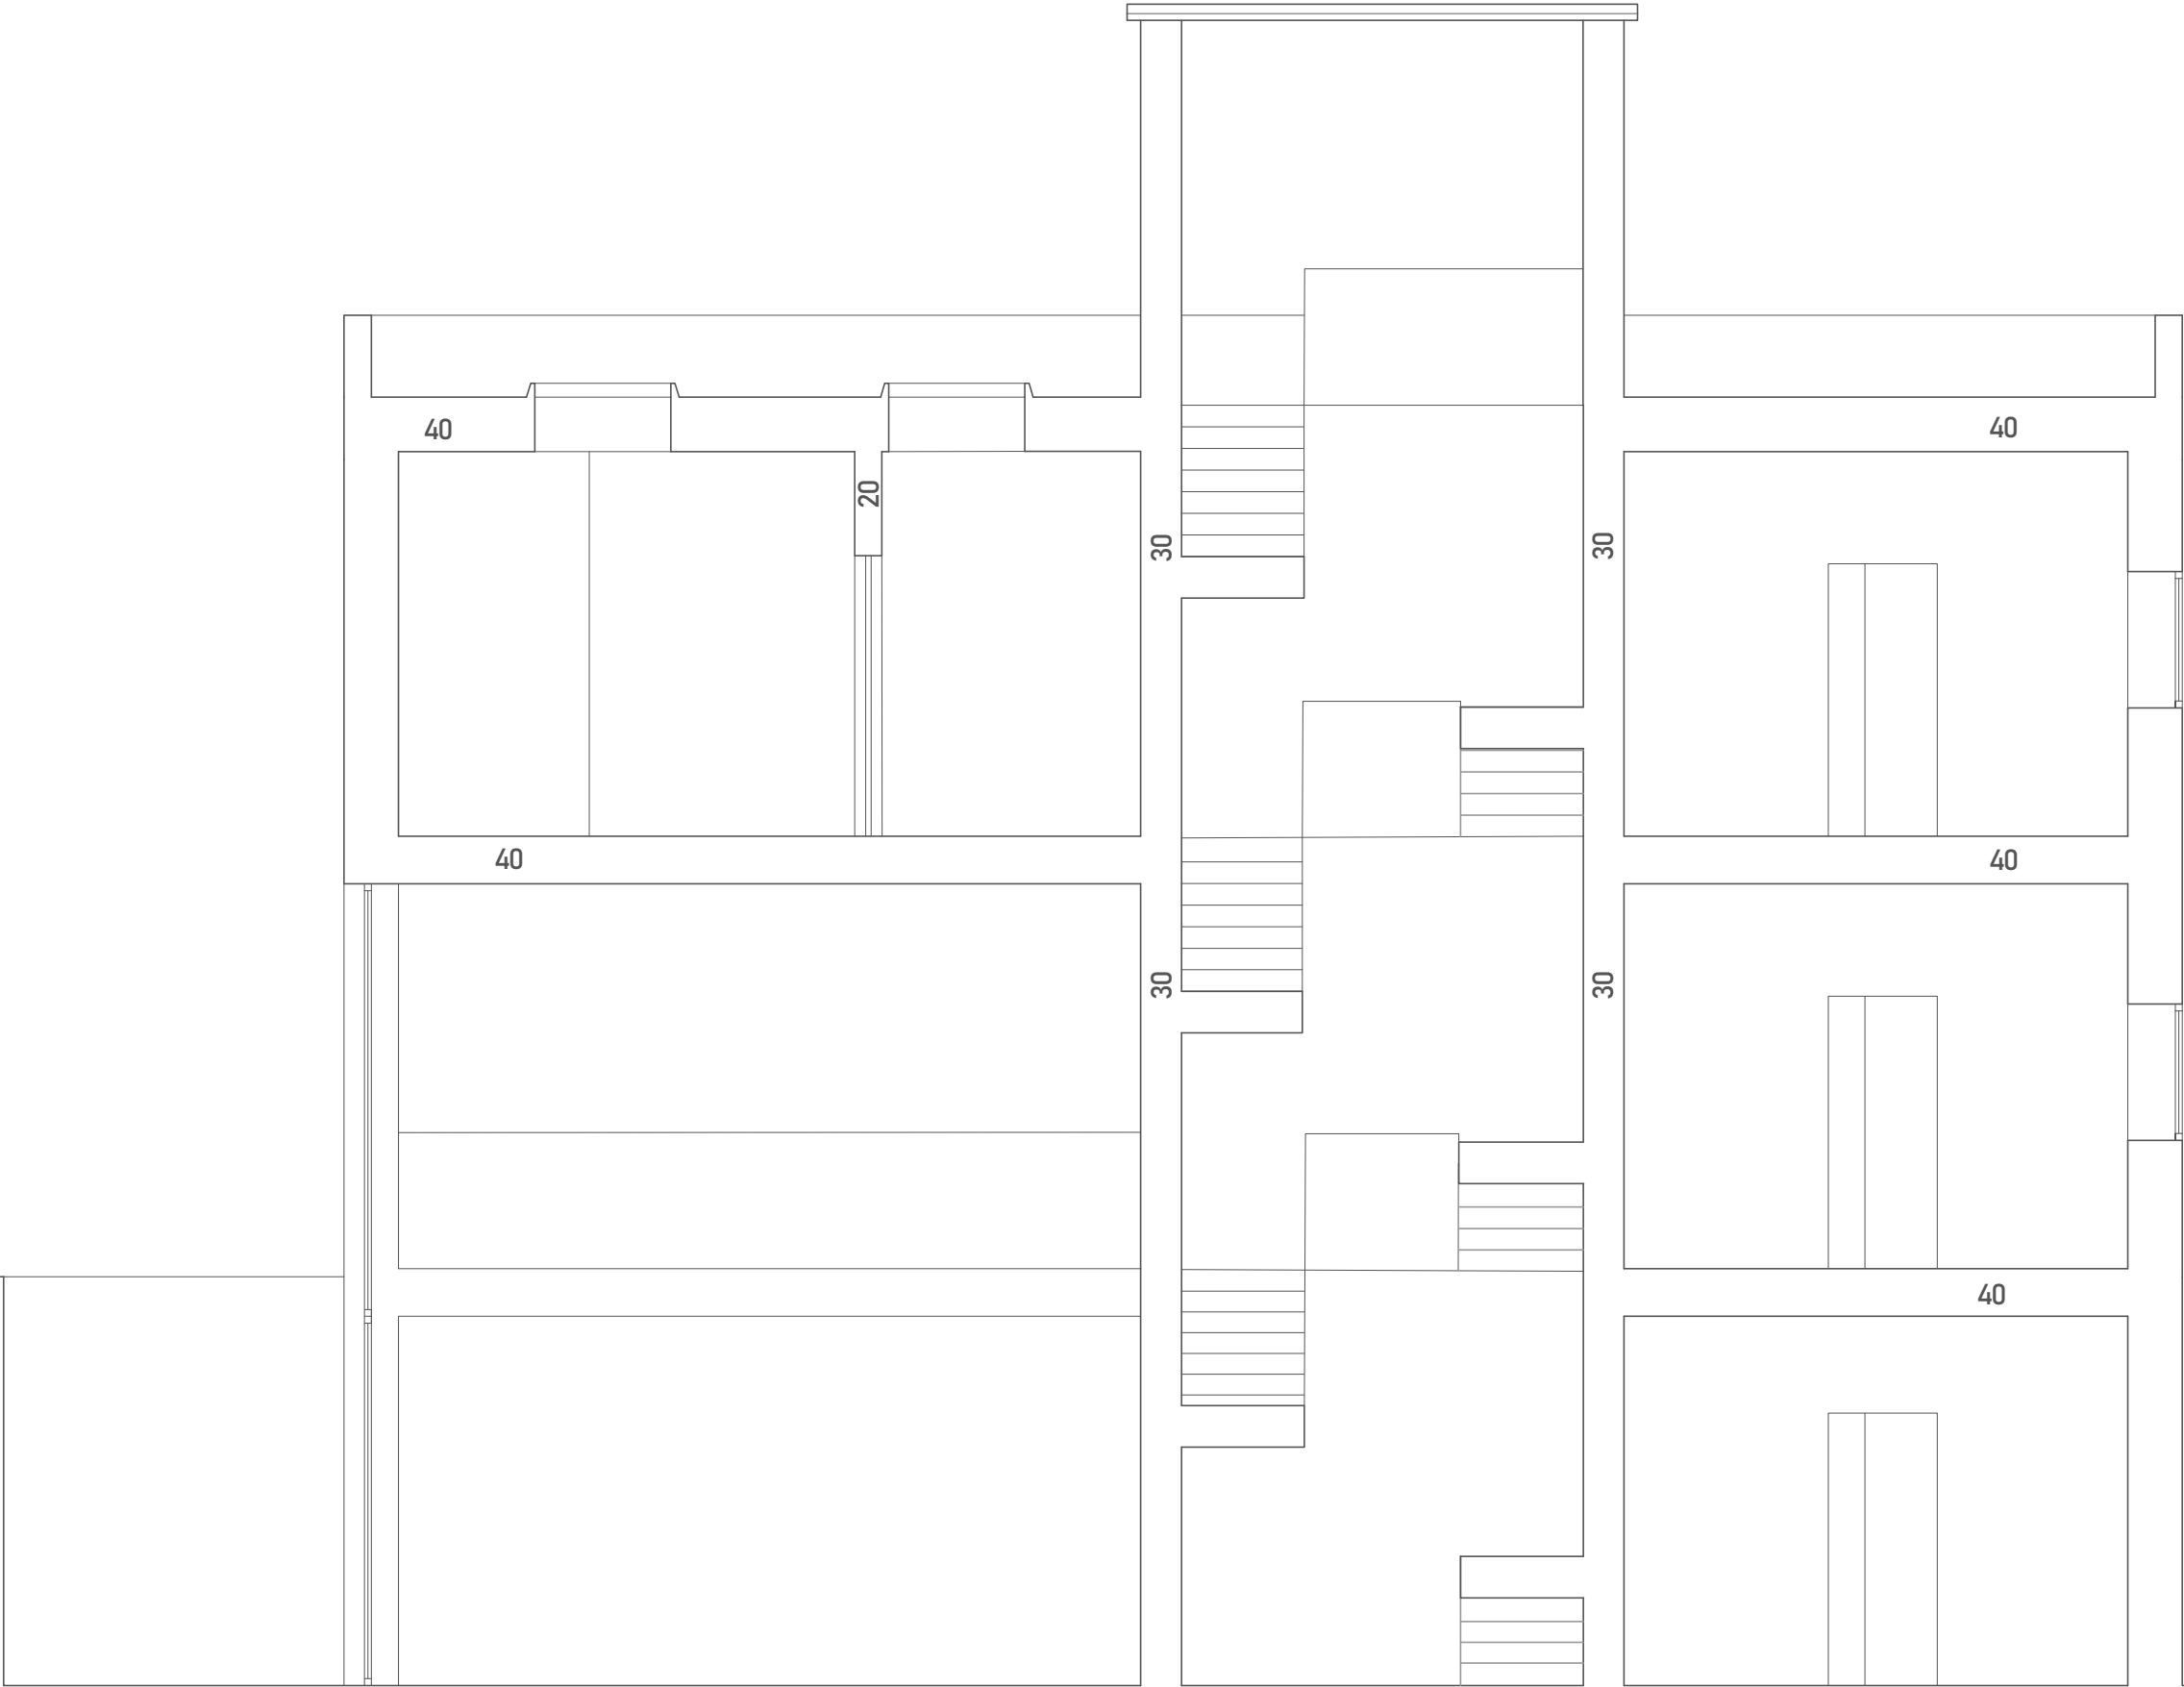


DENOMINACIÓN			
SECCIÓN 1			
PROMOTORES		ESTUDIANTES DE ARQUITECTURA	
ANTONIO VELA COSSIO		JAVIER PÉREZ PELLÓN ALEJANDRO MARTÍN SANCHEZ	
ESCALA	1/50	SUSTITUYE A	PLANO 8

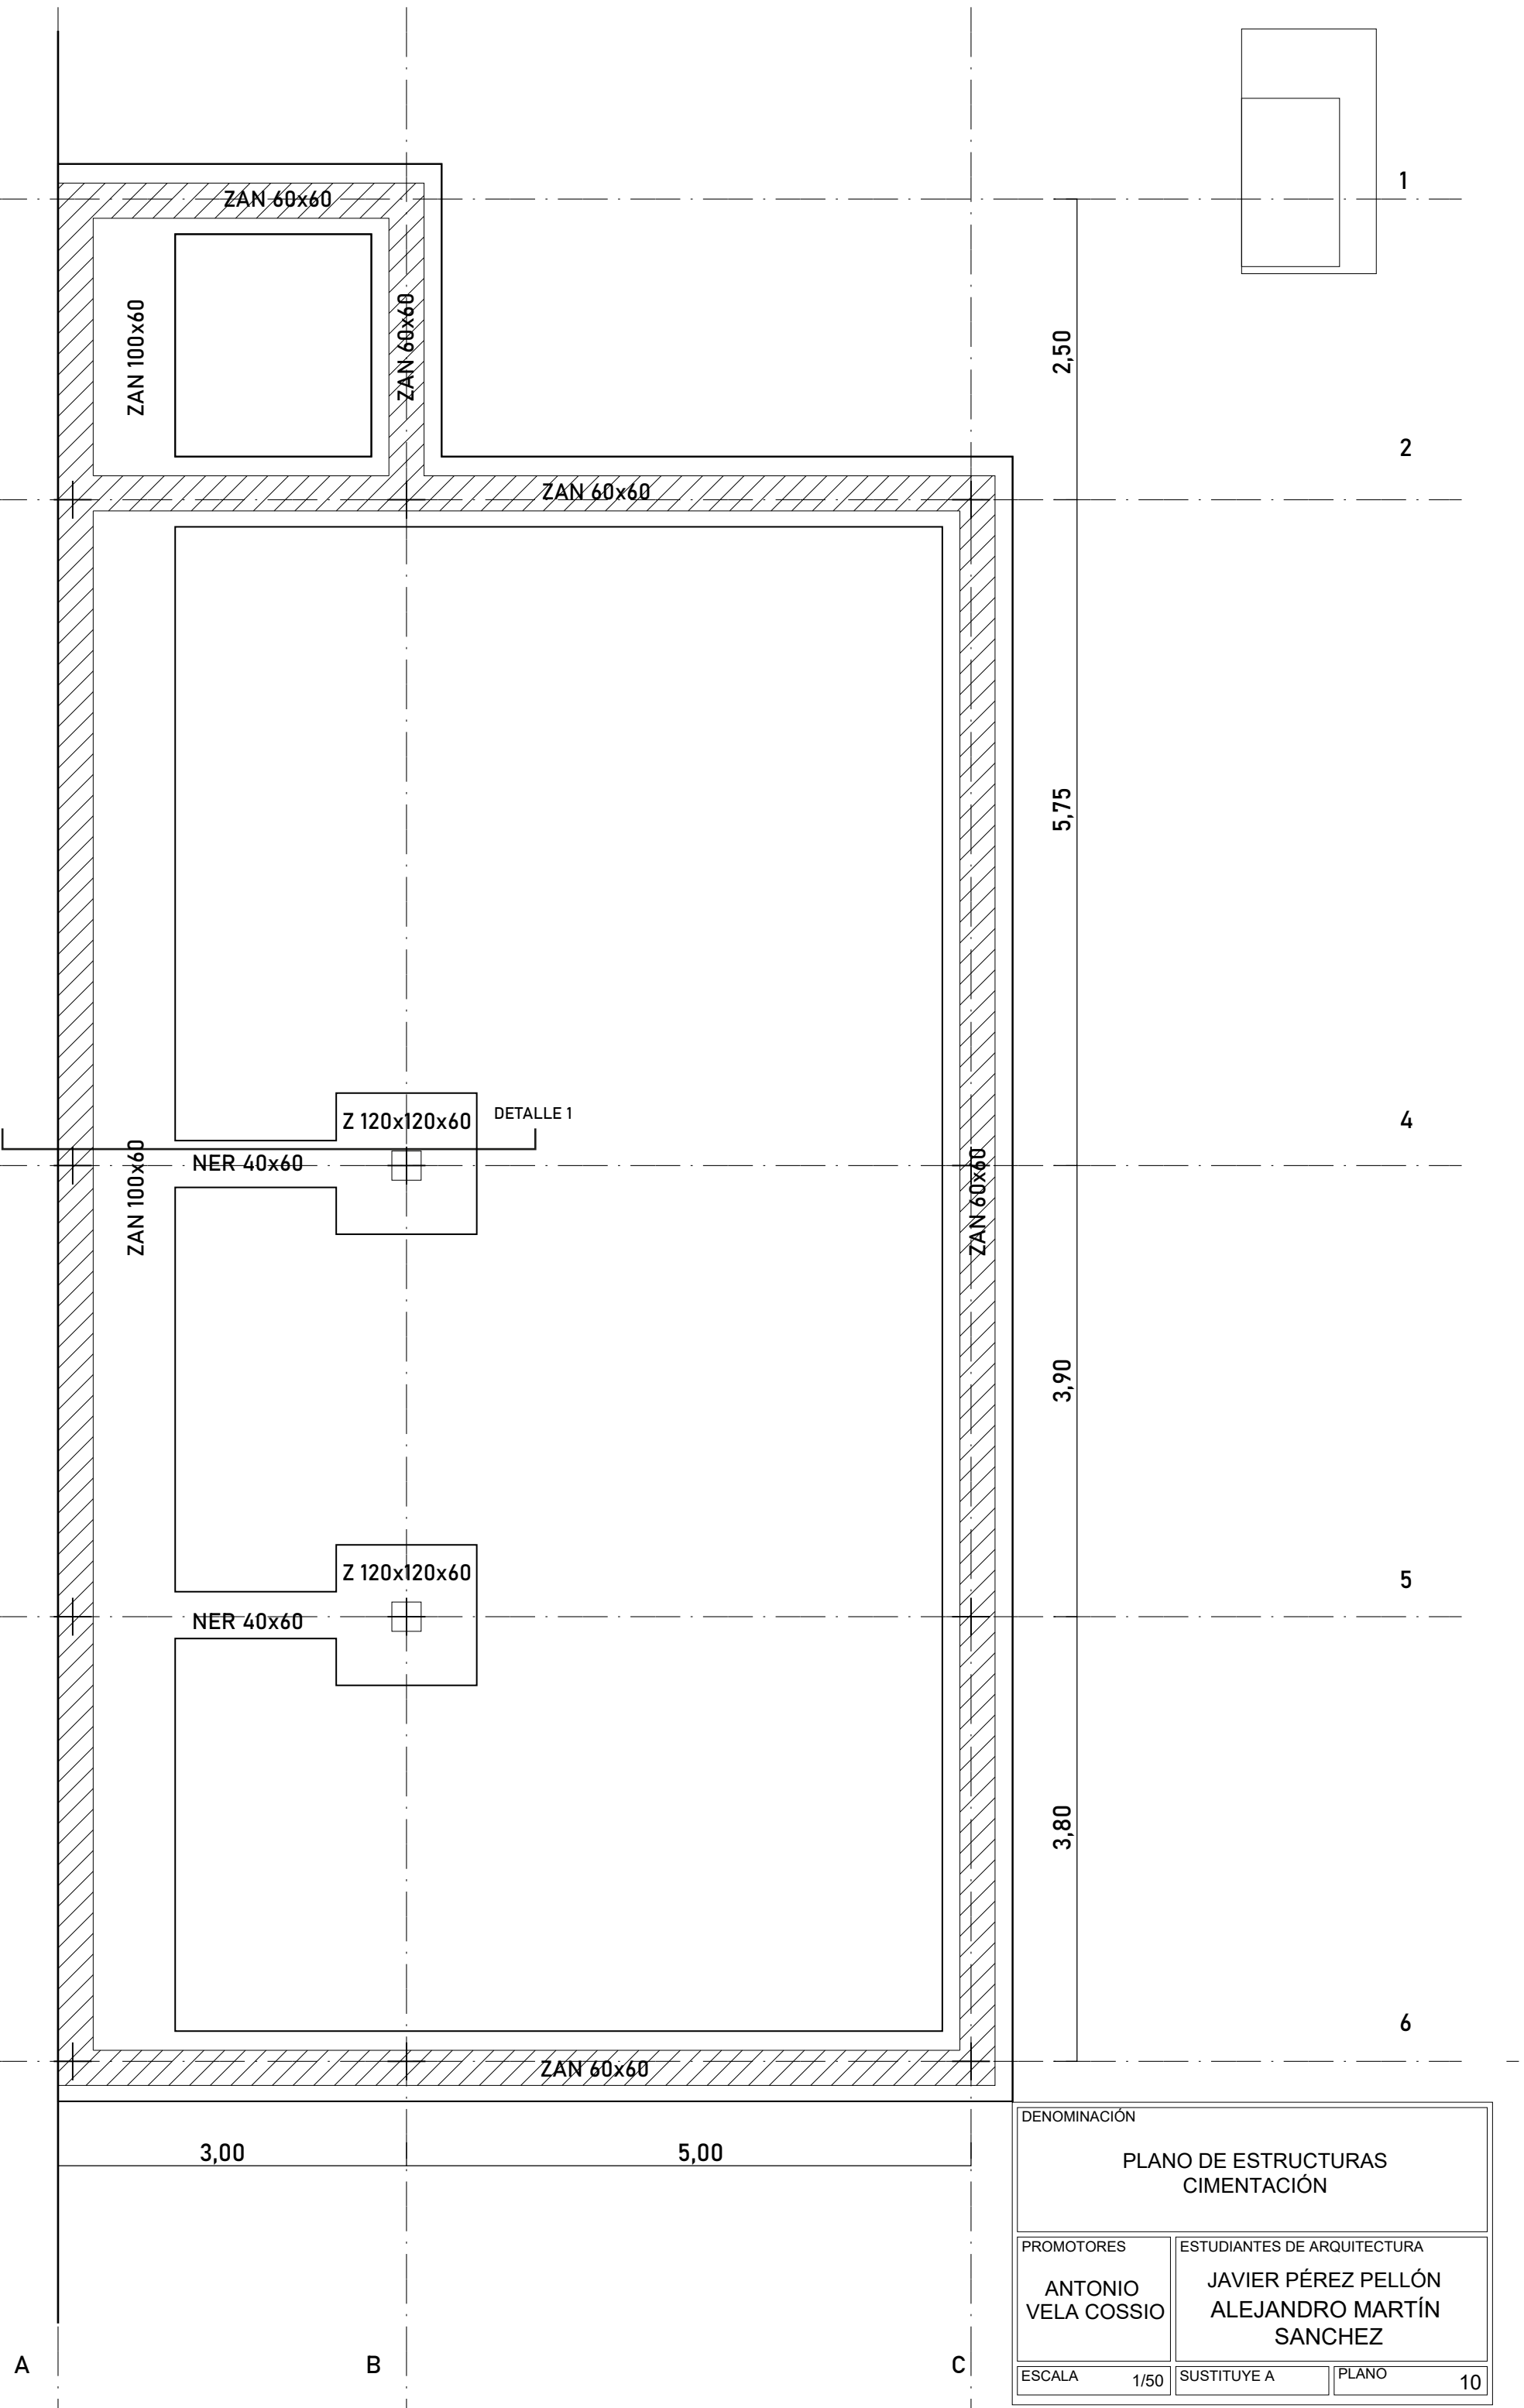

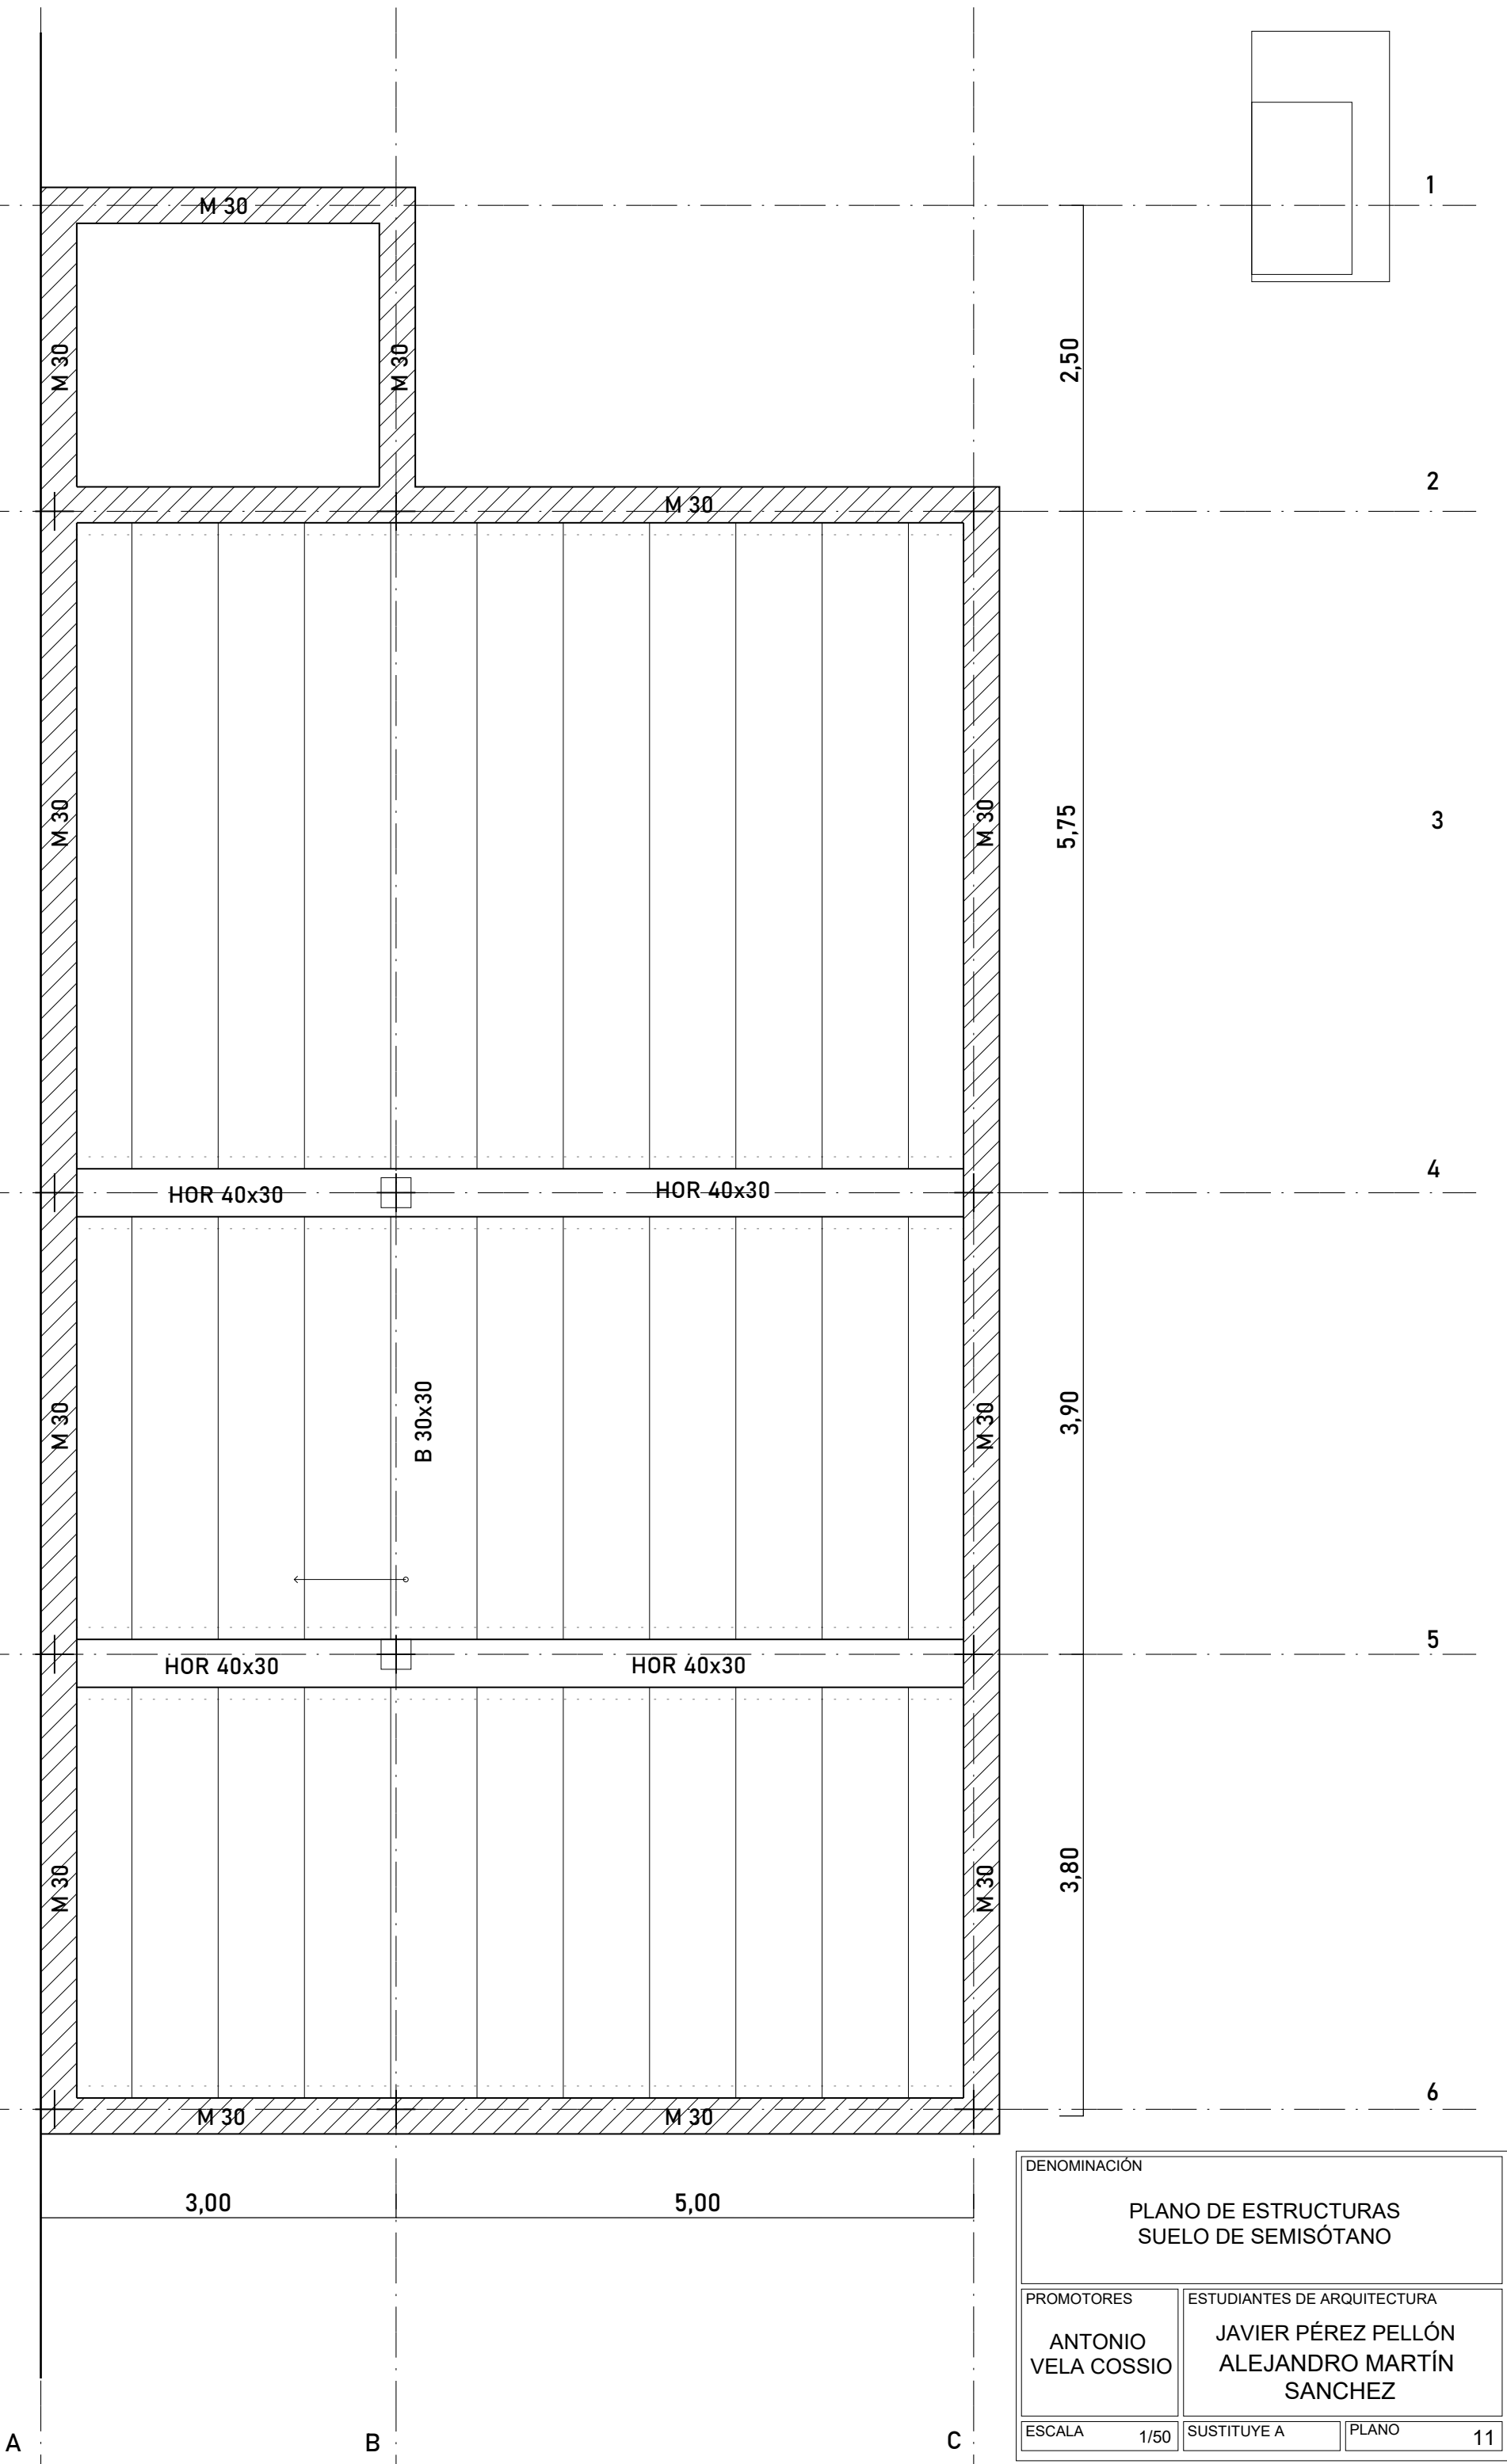

DENOMINACIÓN		
PLANO DE ESTRUCTURAS SUELO DE SEMISÓTANO		
PROMOTORES	ESTUDIANTES DE ARQUITECTURA	
ANTONIO VELA COSSIO	JAVIER PÉREZ PELLÓN ALEJANDRO MARTÍN SANCHEZ	
ESCALA	1/50	SUSTITUYE A
		PLANO
		11

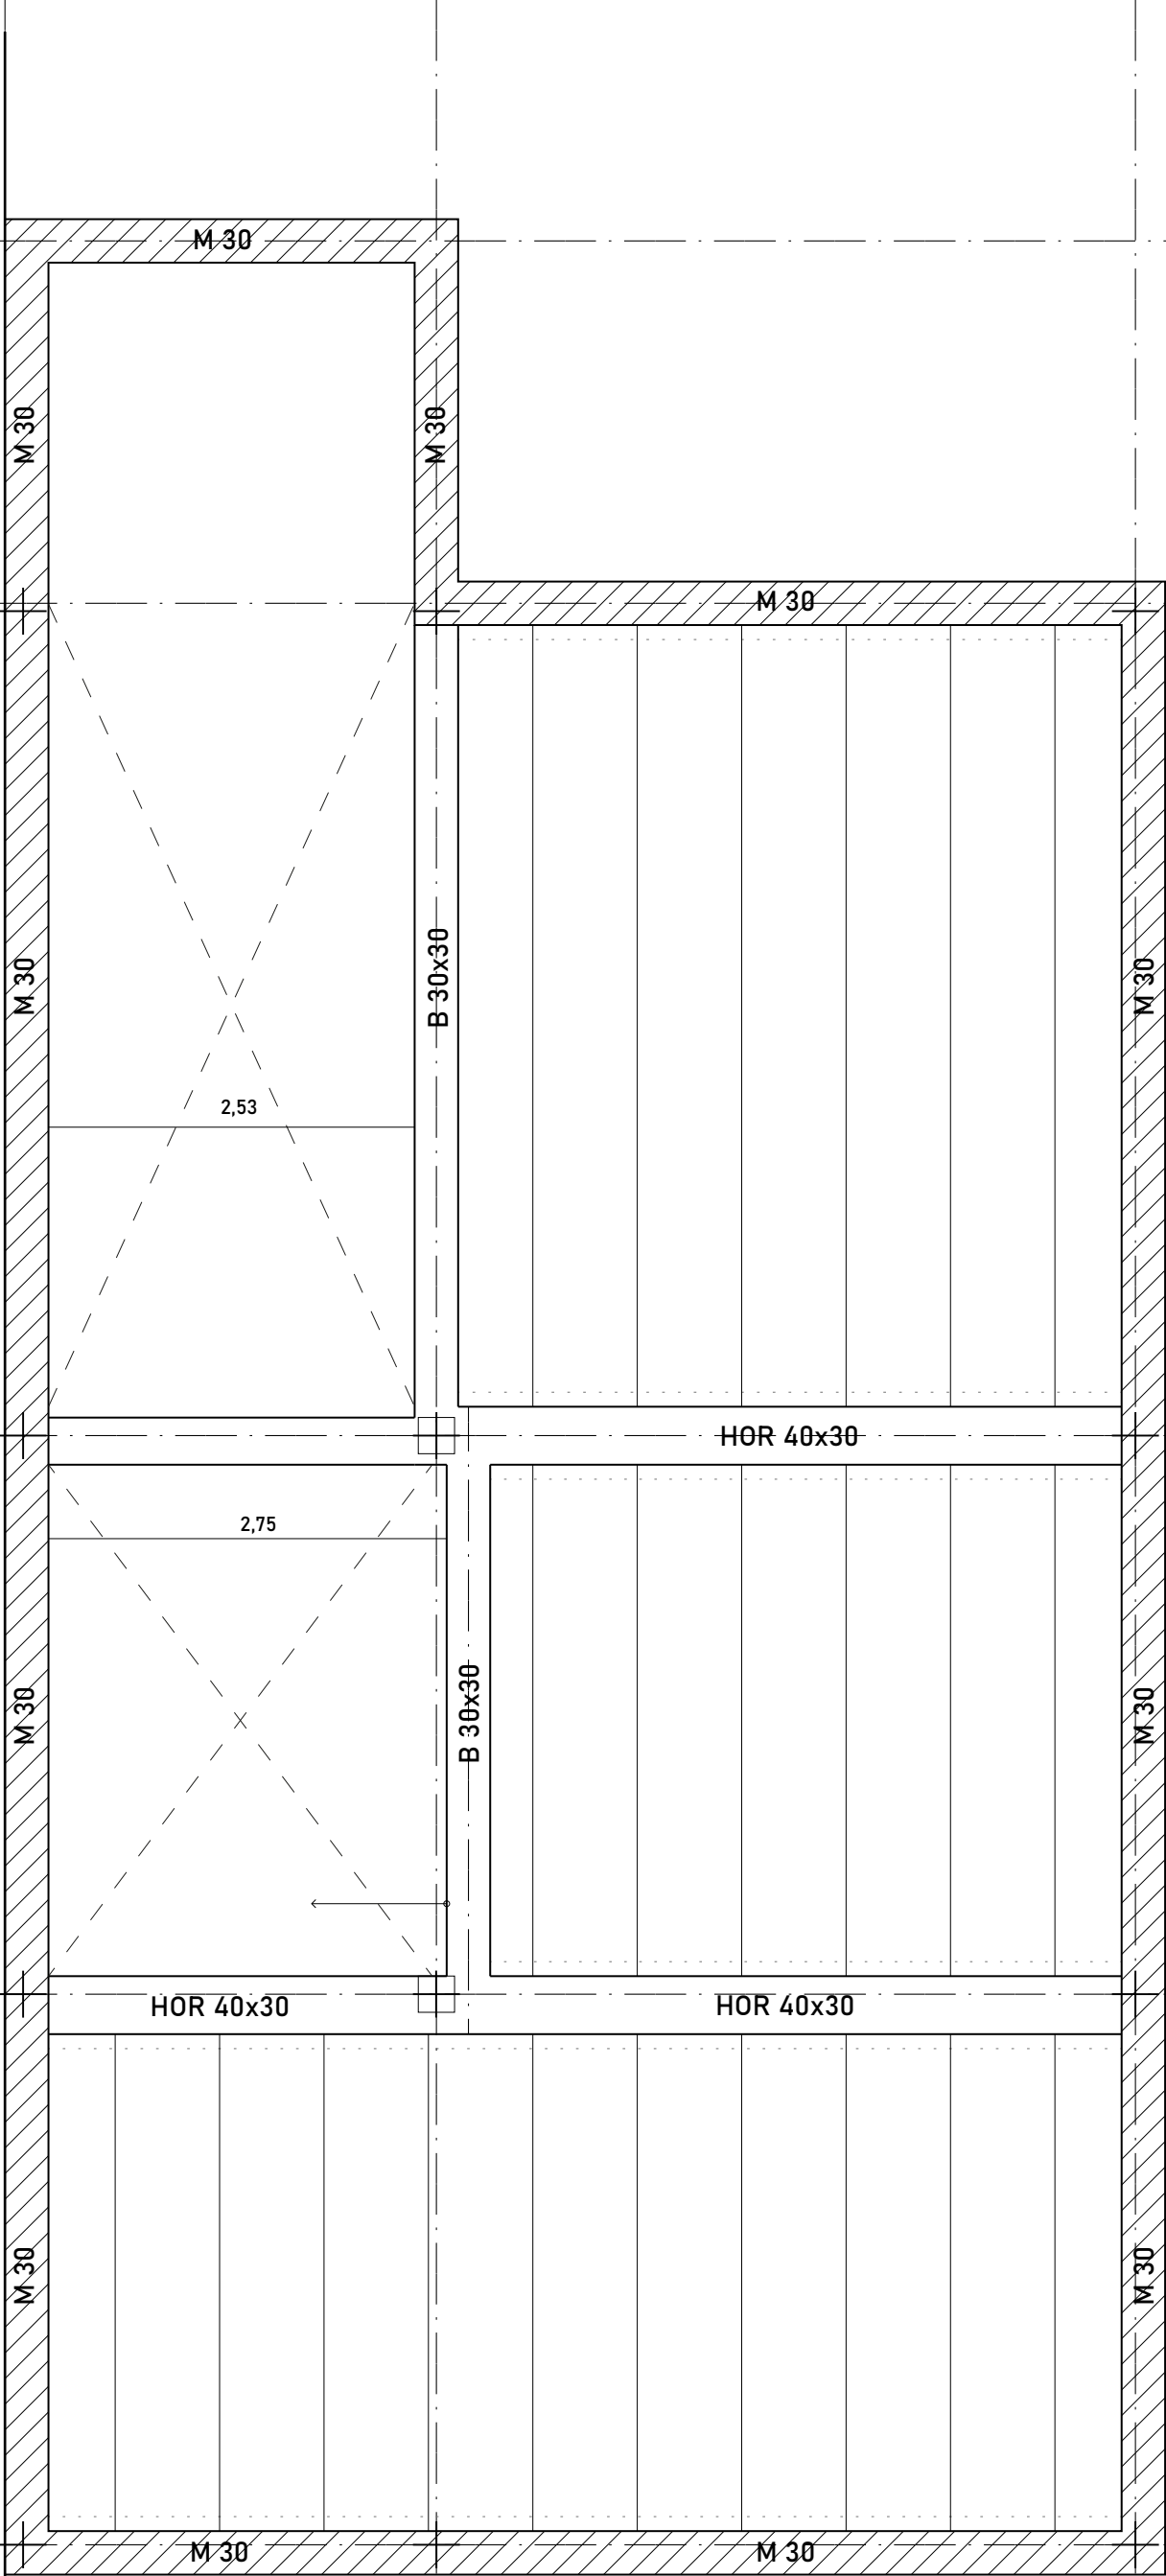


A


B

C

DENOMINACIÓN		
PLANO DE ESTRUCTURAS SUELO DE PLANTA BAJA		
PROMOTORES	ESTUDIANTES DE ARQUITECTURA	
ANTONIO VELA COSSIO	JAVIER PÉREZ PELLÓN ALEJANDRO MARTÍN SANCHEZ	
ESCALA	1/50	SUSTITUYE A
PLANO		12

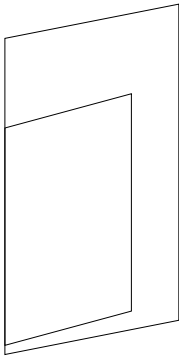

2

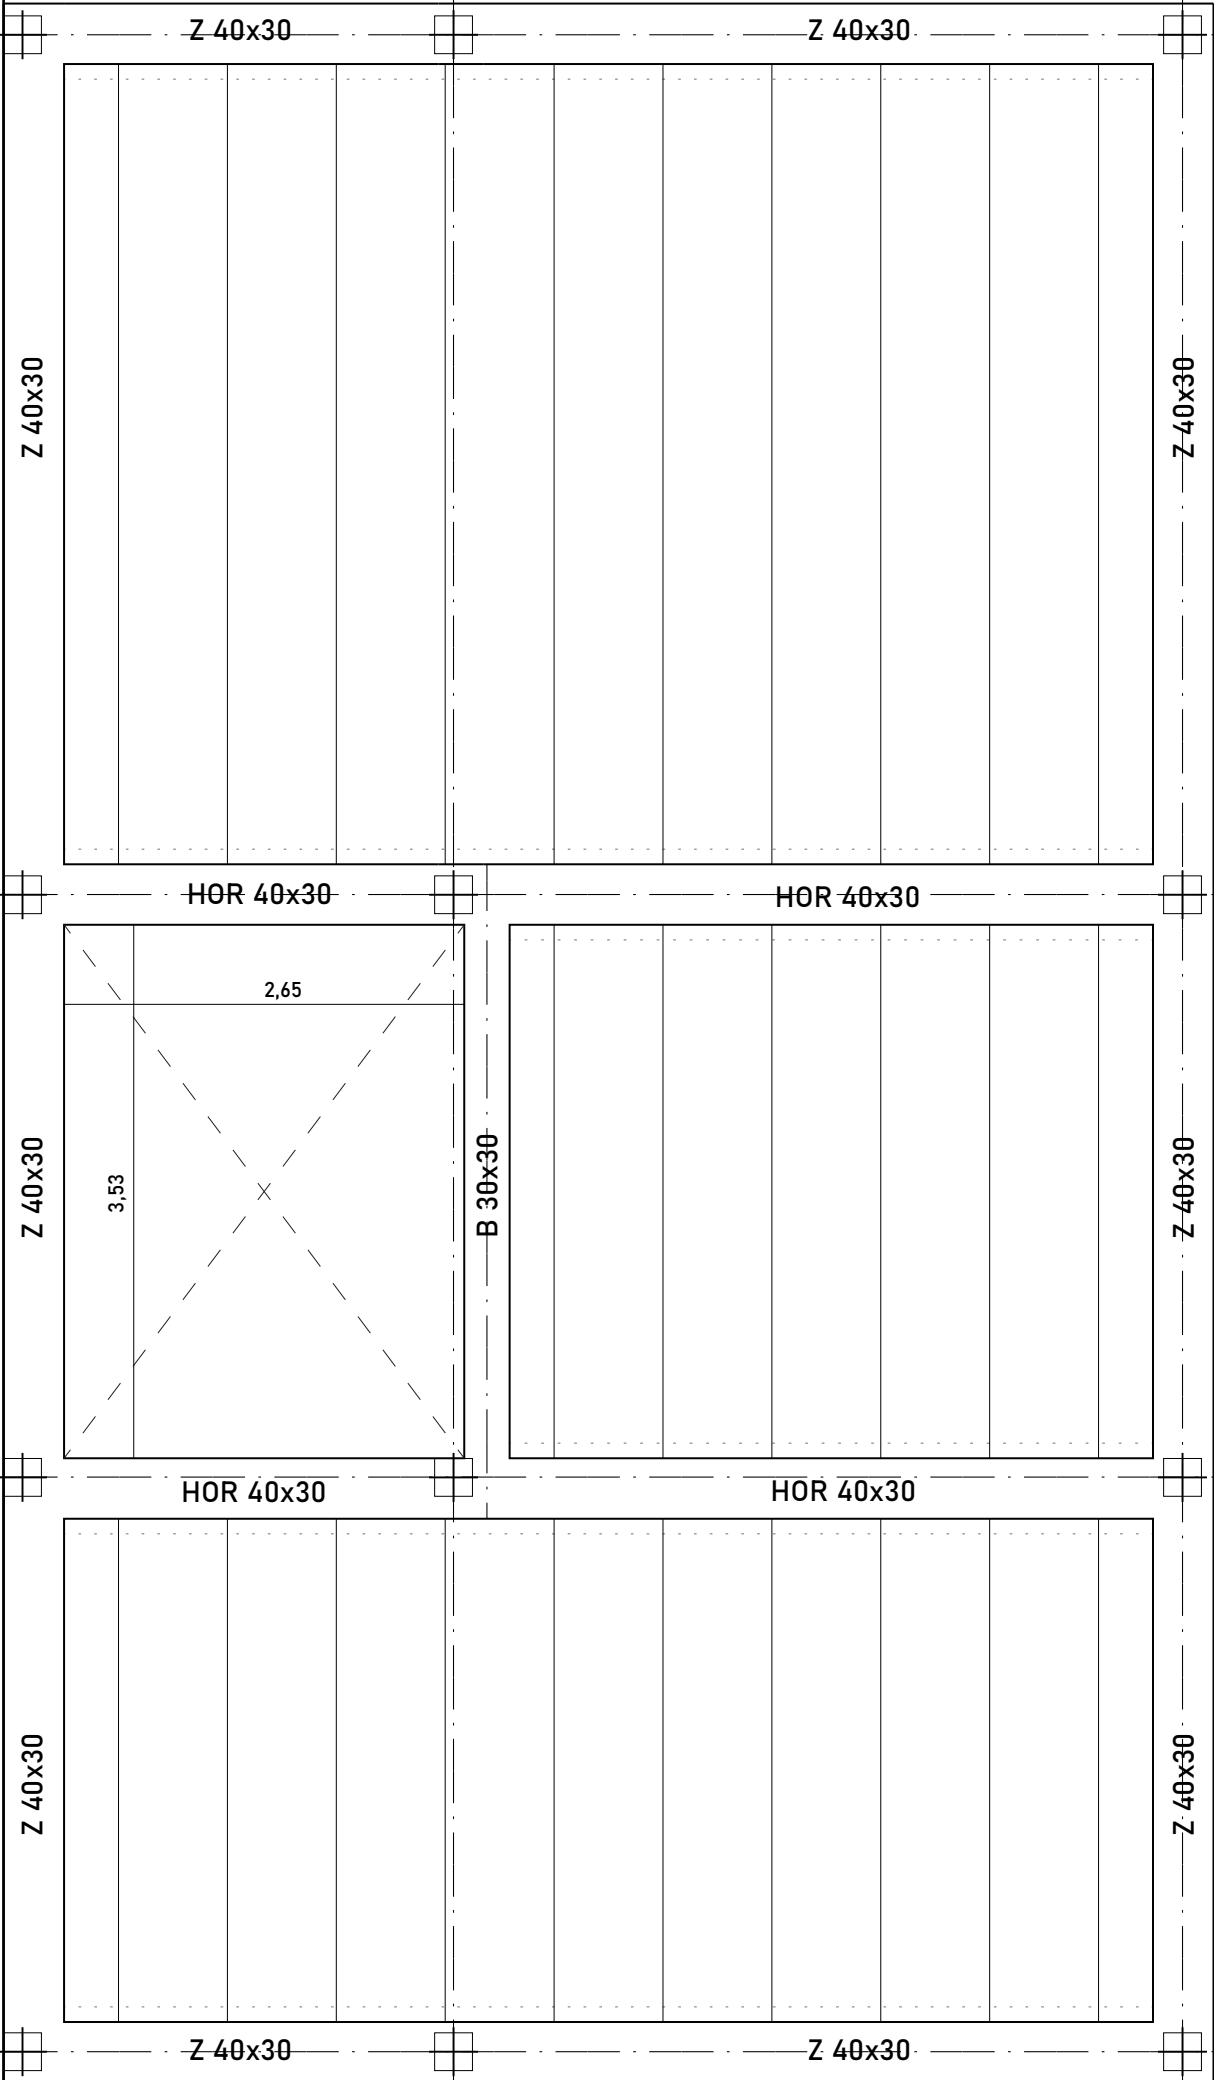

4

5


6

A



B

C

DENOMINACIÓN		
PLANO DE ESTRUCTURAS SUELO DE PLANTA 1		
PROMOTORES	ESTUDIANTES DE ARQUITECTURA	
ANTONIO VELA COSSIO	JAVIER PÉREZ PELLÓN ALEJANDRO MARTÍN SANCHEZ	
ESCALA	1/50	SUSTITUYE A
		PLANO
		13

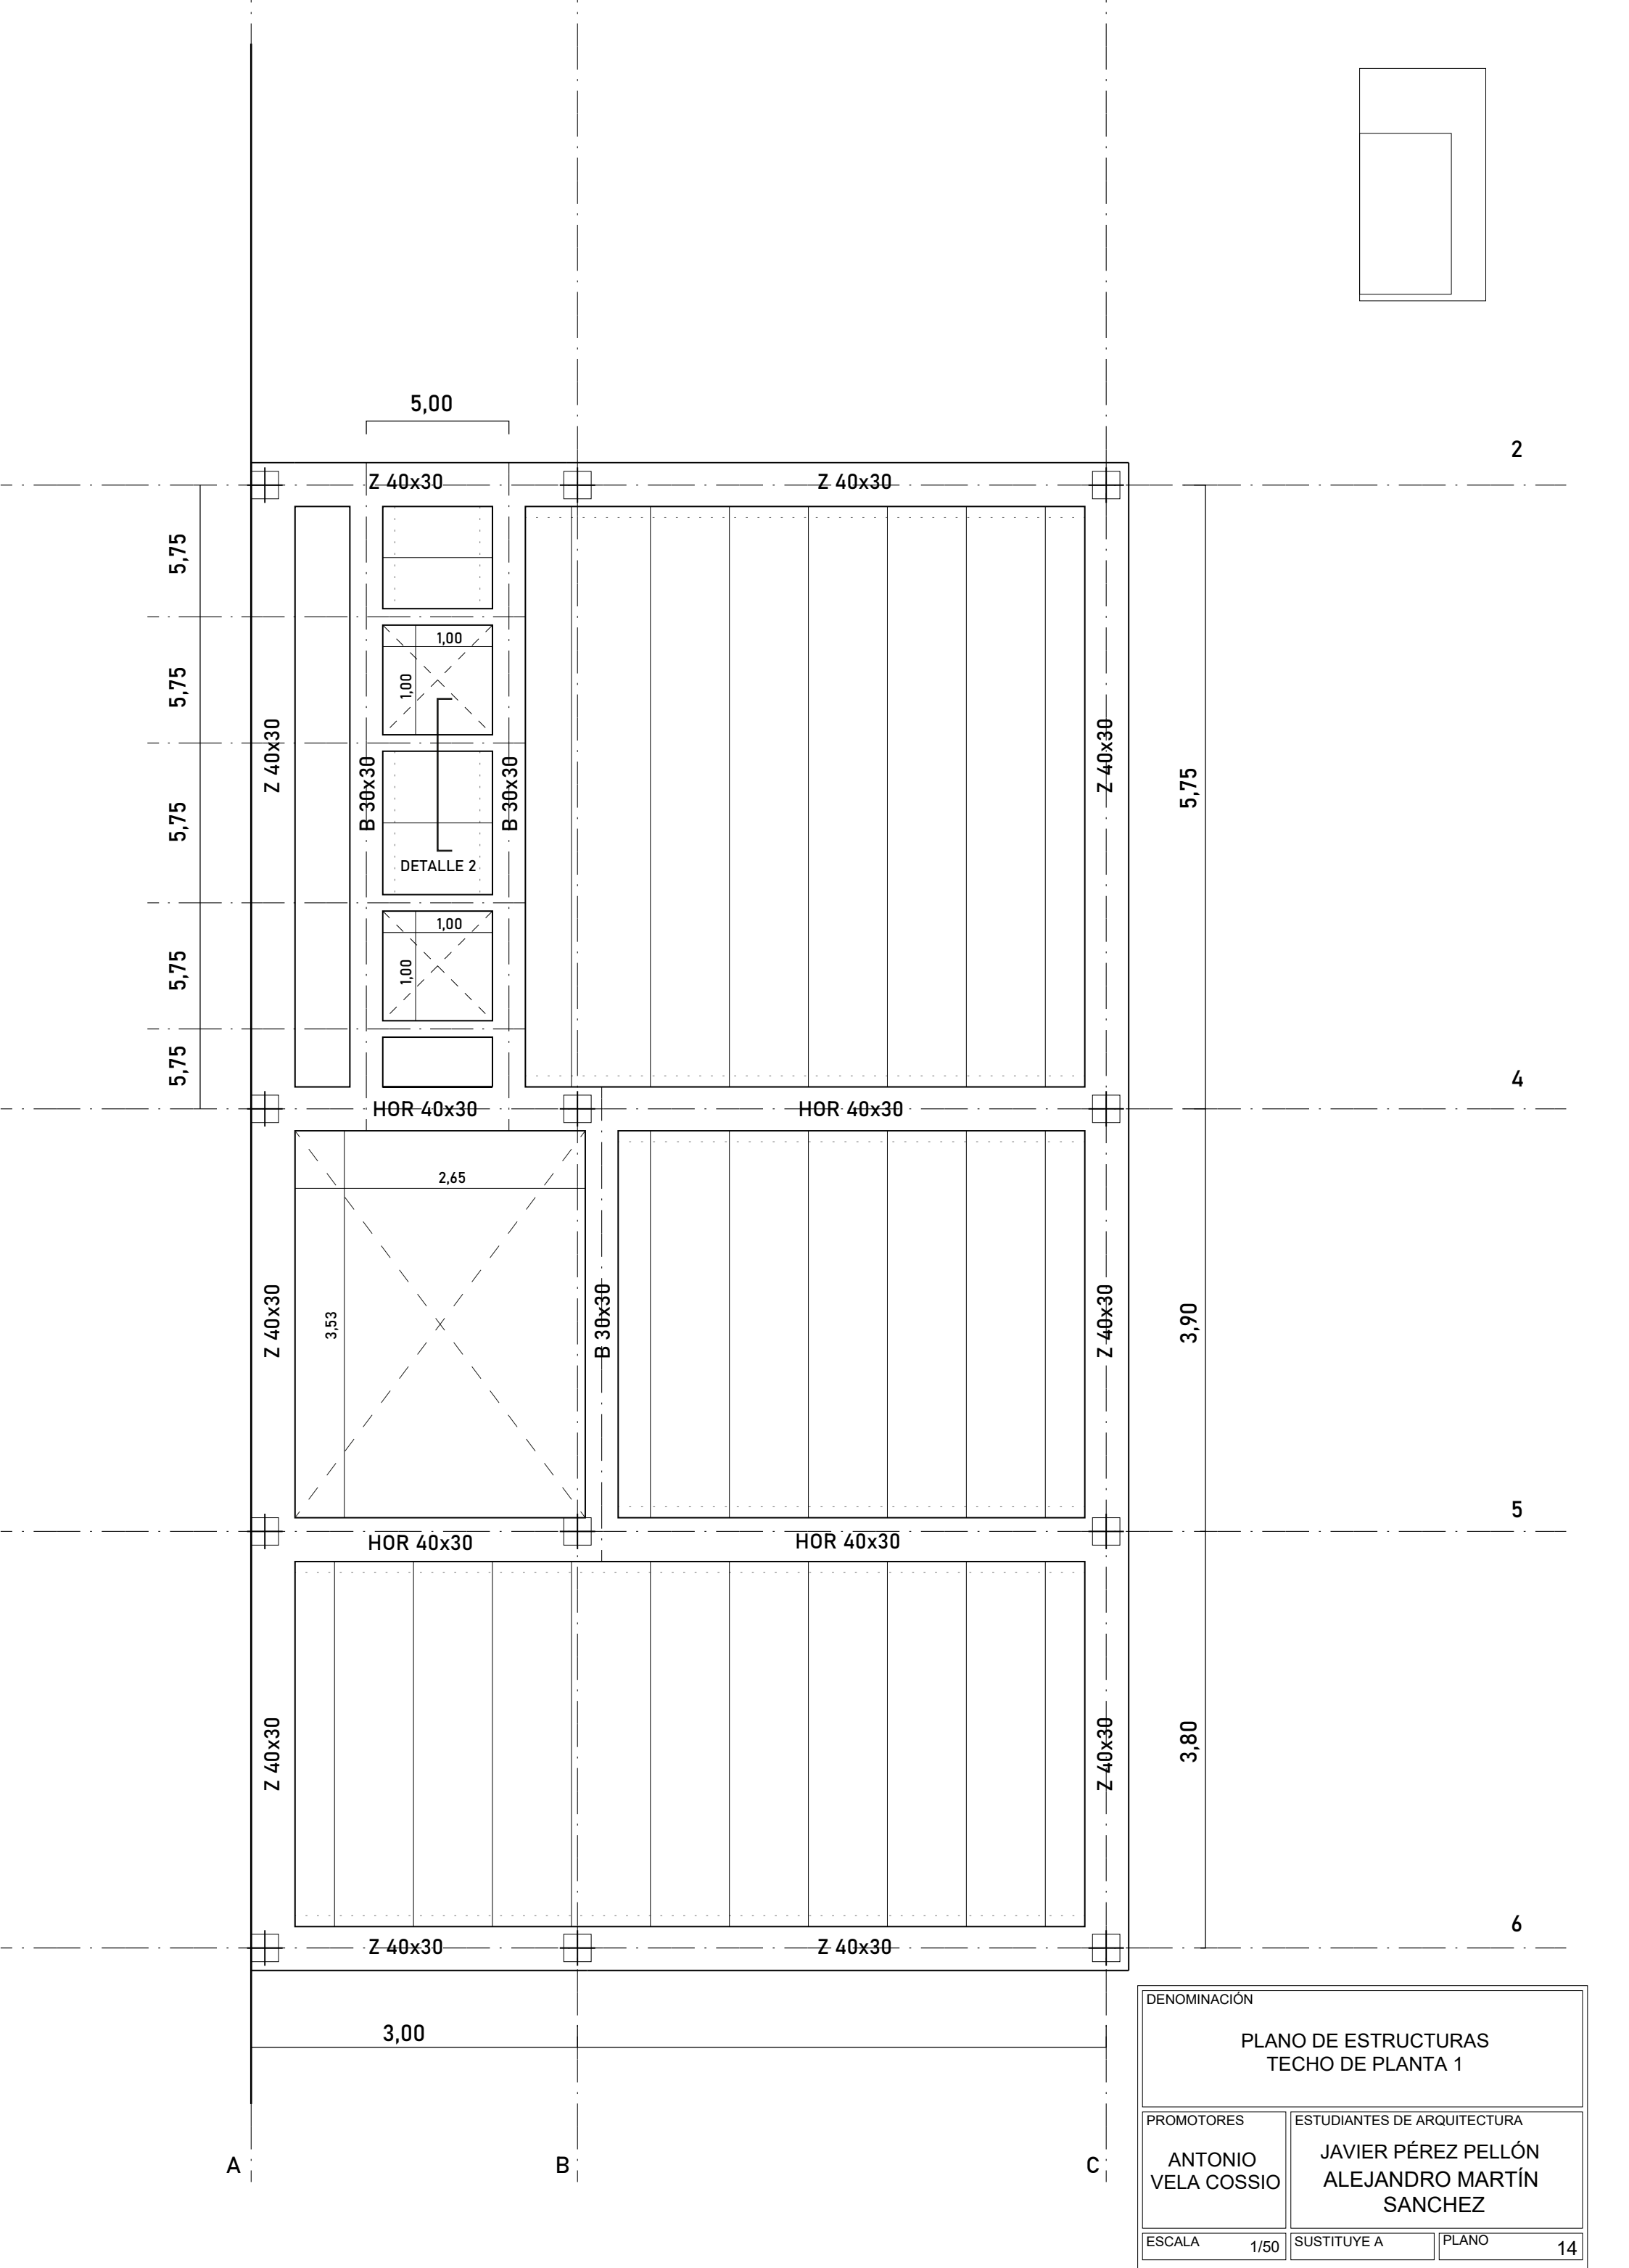

DENOMINACIÓN			
PLANO DE ESTRUCTURAS TECHO DE PLANTA 1			
PROMOTORES		ESTUDIANTES DE ARQUITECTURA	
ANTONIO VELA COSSIO		JAVIER PÉREZ PELLÓN ALEJANDRO MARTÍN SANCHEZ	
ESCALA	1/50	SUSTITUYE A	PLANO 14

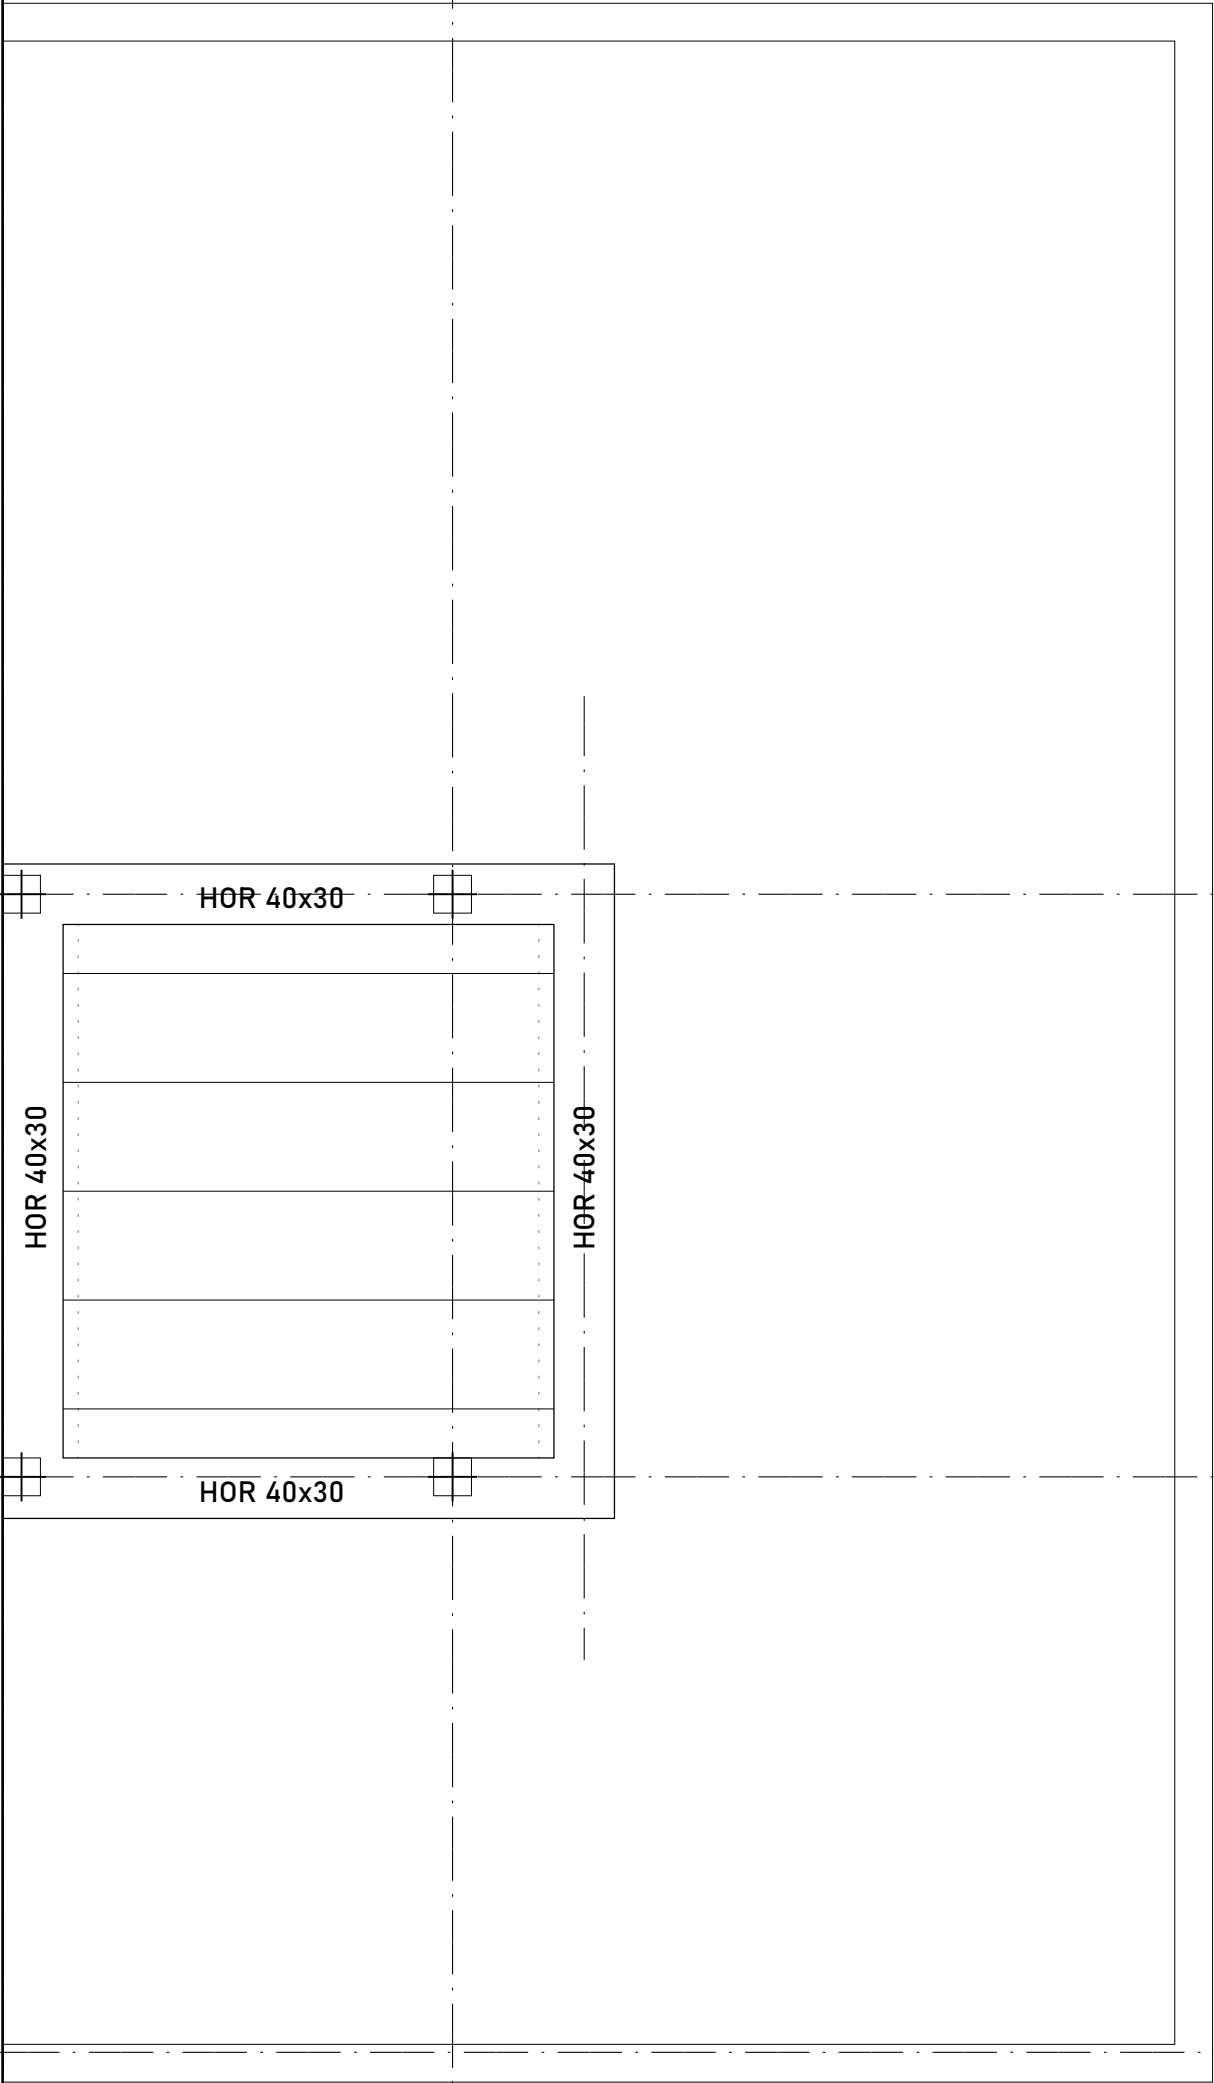 

A

B

4

5

3,90

3,80

HOR 40x30

HOR 40x30

HOR 40x30

HOR 40x30

3,00

DENOMINACIÓN			
PLANO DE ESTRUCTURAS CUEBIERTA			
PROMOTORES		ESTUDIANTES DE ARQUITECTURA	
ANTONIO VELA COSSIO		JAVIER PÉREZ PELLÓN ALEJANDRO MARTÍN SANCHEZ	
ESCALA	1/50	SUSTITUYE A	PLANO 15

MURO DE CONTENCIÓN DE HORMIGÓN ARMADO 250 mm

ARMADURA REDONDOS DEL 12 CADA 150 mm

ESTRIBOS REDONDO DEL 8

ARMADURA LONTUDINAL DEL 16

CAPA DE COMPRESIÓN 50 mm

MALLAZO 4 mm DE 150 x 150

VIGUETA AUTOPORTANTE

BOVEDILLA CERÁMICA

ZAPATA LONGITUDINAL

VIGA CENTRADORA

ESTRIBOS DEL 8

ARMADURA LONGITUDINAL DEL 20


ARRANQUE DE PILAR REDONDOS DEL 16

ZAPATA LONGITUDINAL

PARRILLA DE ZAPATA DEL 16

SEPARADORES DE HORMIGÓN

HORMIGÓN DE LIMPIEZA

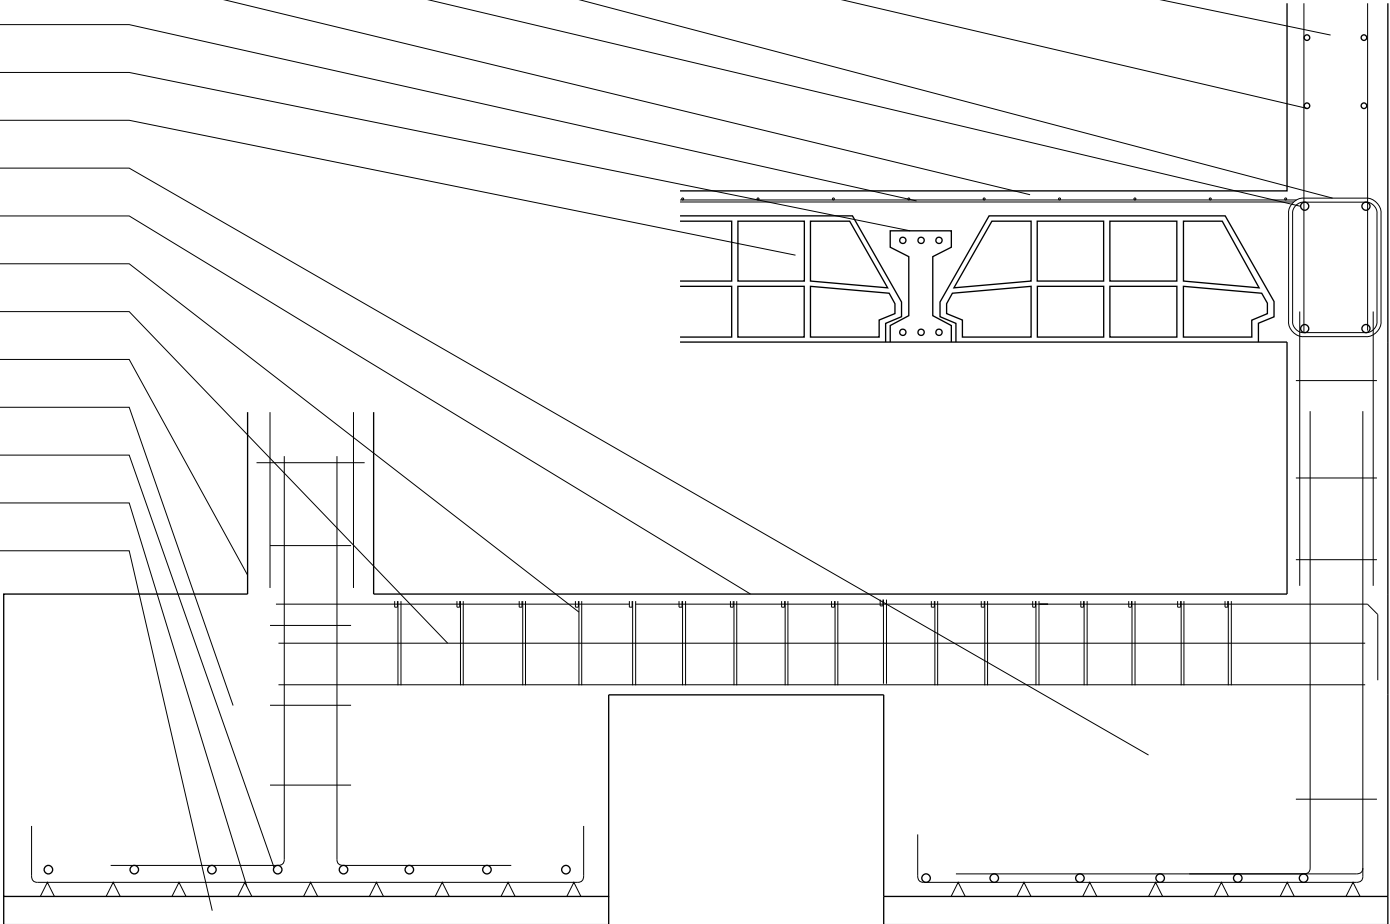

1/15

VIDRIO

MARCO DE VENTANA DE CUBIERTA

CANTO REDONDEADO 15 mm

ESTRIVOS REDONDO DEL 8

MORTERO DE CEMENTO

AISLAMIENTO XPS 100 mm

2 LÁMINAS DE BETÚN MODIFICADO 5 kg

HORMIGÓN DE PENDIENTES

CAPA DE COMPRESIÓN 50 mm

MALLAZO 4mm


BOVEDILLA CERÁMICA

ARMADO LONGITUDINAL REDONDO DEL 16

AISLAMIENTO XPS 120 mm

PERFILES METÁLICOS DE SUJECCIÓN

PLACA DE CARTÓN YESO 10 mm

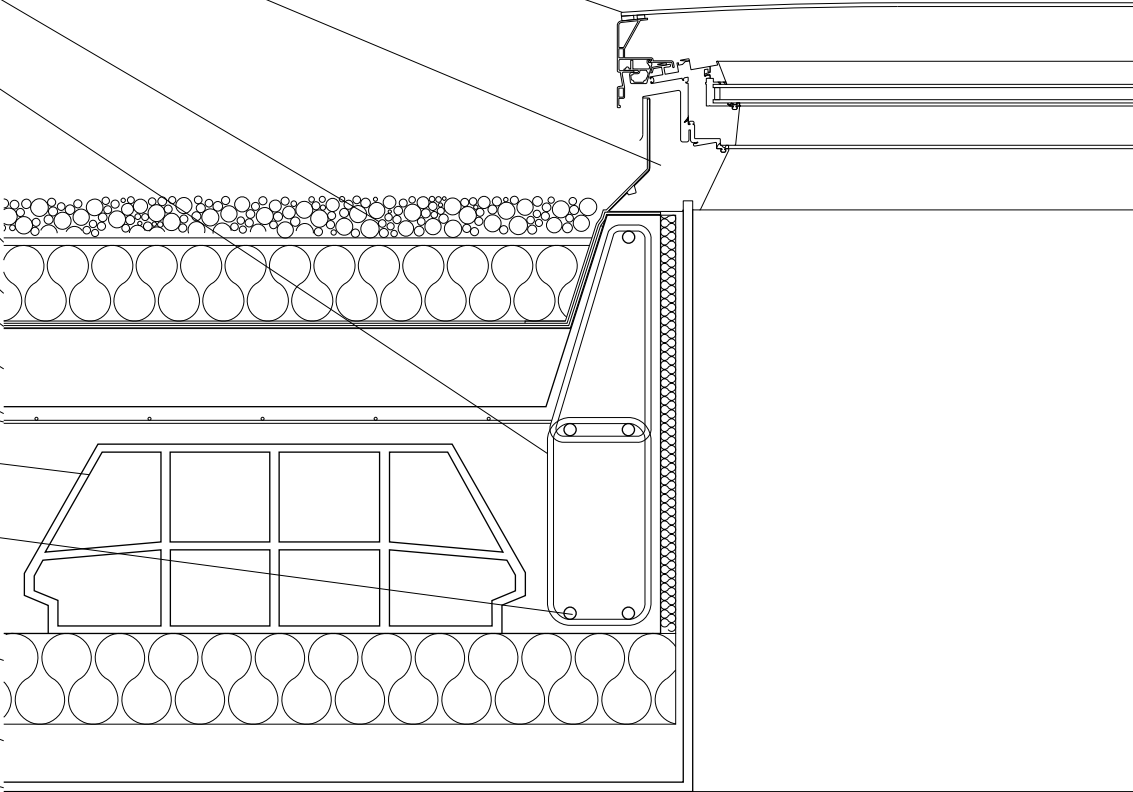

1/10

DENOMINACIÓN			
DETALLES 1 Y 2			
PROMOTORES	ESTUDIANTES DE ARQUITECTURA		
ANTONIO VELA COSSIO	JAVIER PÉREZ PELLÓN ALEJANDRO MARTÍN SANCHEZ		
ESCALA	SUSTITUYE A	PLANO	16

FÁBRICA DE MEDIO PIE LADRILLO CARAVISTA

ENFOSCADO DE CEMENTO 10 mm

AISLAMIENTO XPS 120 mm

CÁMARA DE AIRE 100 mm

PERFILERÍA DE ACERO GAVANIZADO

L 50

DOBLE PLACA DE CARTÓN YESO 2 x 12,5 mm

PREMARCO DE MADERA 30 x 100 mm

RELLENO DE ESPUMA DE POLIURETANO


CAJÓN DE PERSIANA

AISLAMAMIENTO DEL CAJÓN DE PERSIANA

CARGADERO PREFABRICADO REVESTIDO DE CERÁMICA

CARPINTERÍA DE ALUMINIO LACADO CON RPT


DOBLE VIDRIO CON CÁMARA DE AIRE 4 + 12 + 6 mm

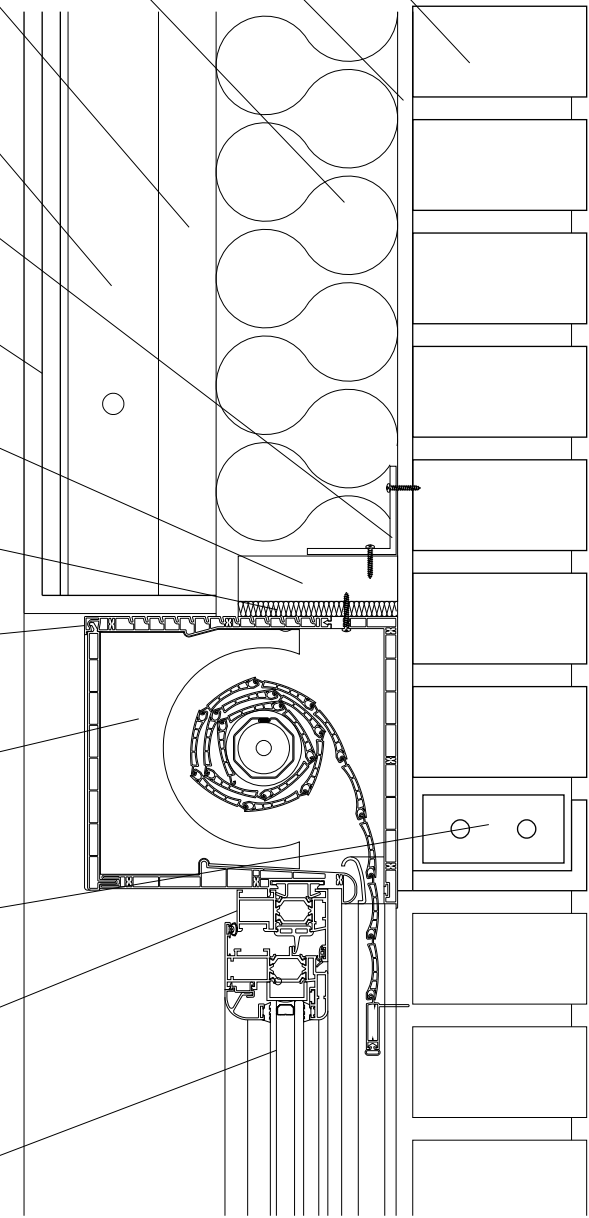

DENOMINACIÓN			
DETALLE 3			
PROMOTORES		ESTUDIANTES DE ARQUITECTURA	
ANTONIO VELA COSSIO		JAVIER PÉREZ PELLÓN ALEJANDRO MARTÍN SANCHEZ	
ESCALA	1/5	SUSTITUYE A	PLANO 17



1/5

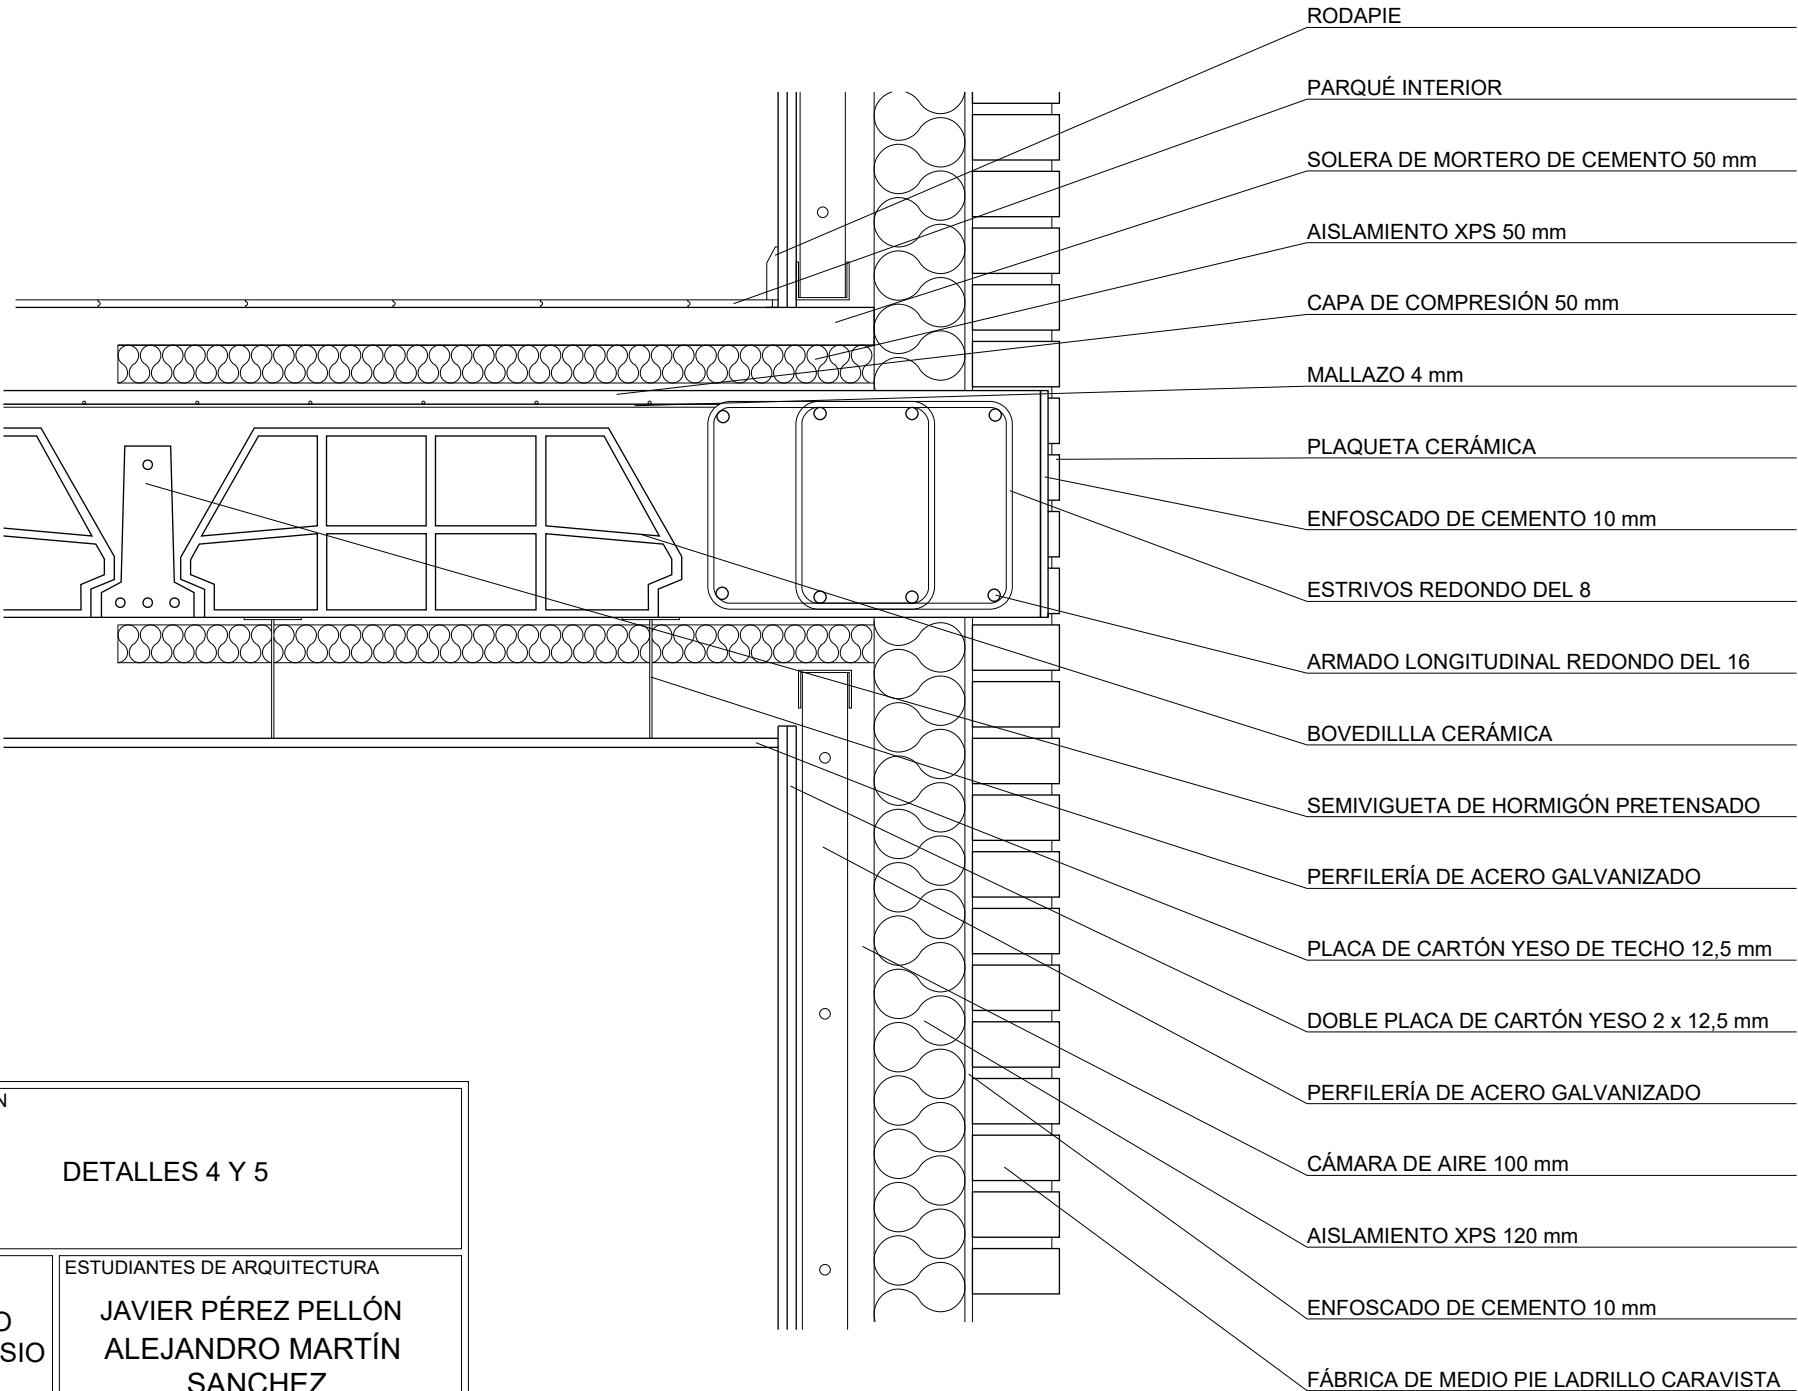

1/10

DENOMINACIÓN			
DETALLES 4 Y 5			
PROMOTORES	ESTUDIANTES DE ARQUITECTURA		
ANTONIO VELA COSSIO	JAVIER PÉREZ PELLÓN ALEJANDRO MARTÍN SANCHEZ		
ESCALA	SUSTITUYE A	PLANO	18